





- NOTES:**
1. ALL LEVELS ARE IN METRES ABOVE DATUM UNLESS STATED OTHERWISE.
 2. DO NOT SCALE FROM THIS DRAWING. ALL DIMENSIONS INDICATED ARE IN METRES UNLESS OTHERWISE STATED. VALIDATE ALL MEASUREMENTS ON SITE.
 3. ANY DISCREPANCIES BETWEEN THE DRAWINGS AND OTHER DOCUMENTS SHOULD BE BROUGHT TO THE ATTENTION OF THE ENGINEER.
 4. THIS DRAWING IS NOT AN INSTALLATION DRAWING. IT IS THE CONTRACTORS RESPONSIBILITY TO MAKE FINAL COORDINATED INSTALLATION SHOP DRAWINGS.
 5. THE CONTENTS OF THIS DRAWING SHALL BE READ IN CONJUNCTION WITH THE CURRENT EDITIONS OF ARCHITECTURAL, CIVIL, STRUCTURAL, MECHANICAL, ELECTRICAL, SECURITY, TELECOMS DRAWINGS AND ALL RELEVANT SECTIONS OF THE SPECIFICATIONS.

ADDITIONAL NOTES:

1. FOR REFERENCE OF SPECIAL DETAILS, PLEASE SEE SHEET STB1A-1.0-C-8530-SDT TO STB1A-1.0-C-8532-SDT.
2. CABLE PULLING EXERCISE TO BE CONDUCTED BY SPC. CHAMBER SIZES ARE AS ELECTRICAL ENGINEER DESIGN.
3. FOR HIGH VOLTAGE DUCT SIZES REFER TO DETAIL STB1A-1.0-C-8630-SDT. ALL MV AND HV DUCTS TO BE HIGH-DENSITY POLYETHYLENE (HDPE) DUCT MATERIAL.
5. FINAL CABLE PULLING EXERCISE TO BE CARRIED OUT BY PMC

LEGEND

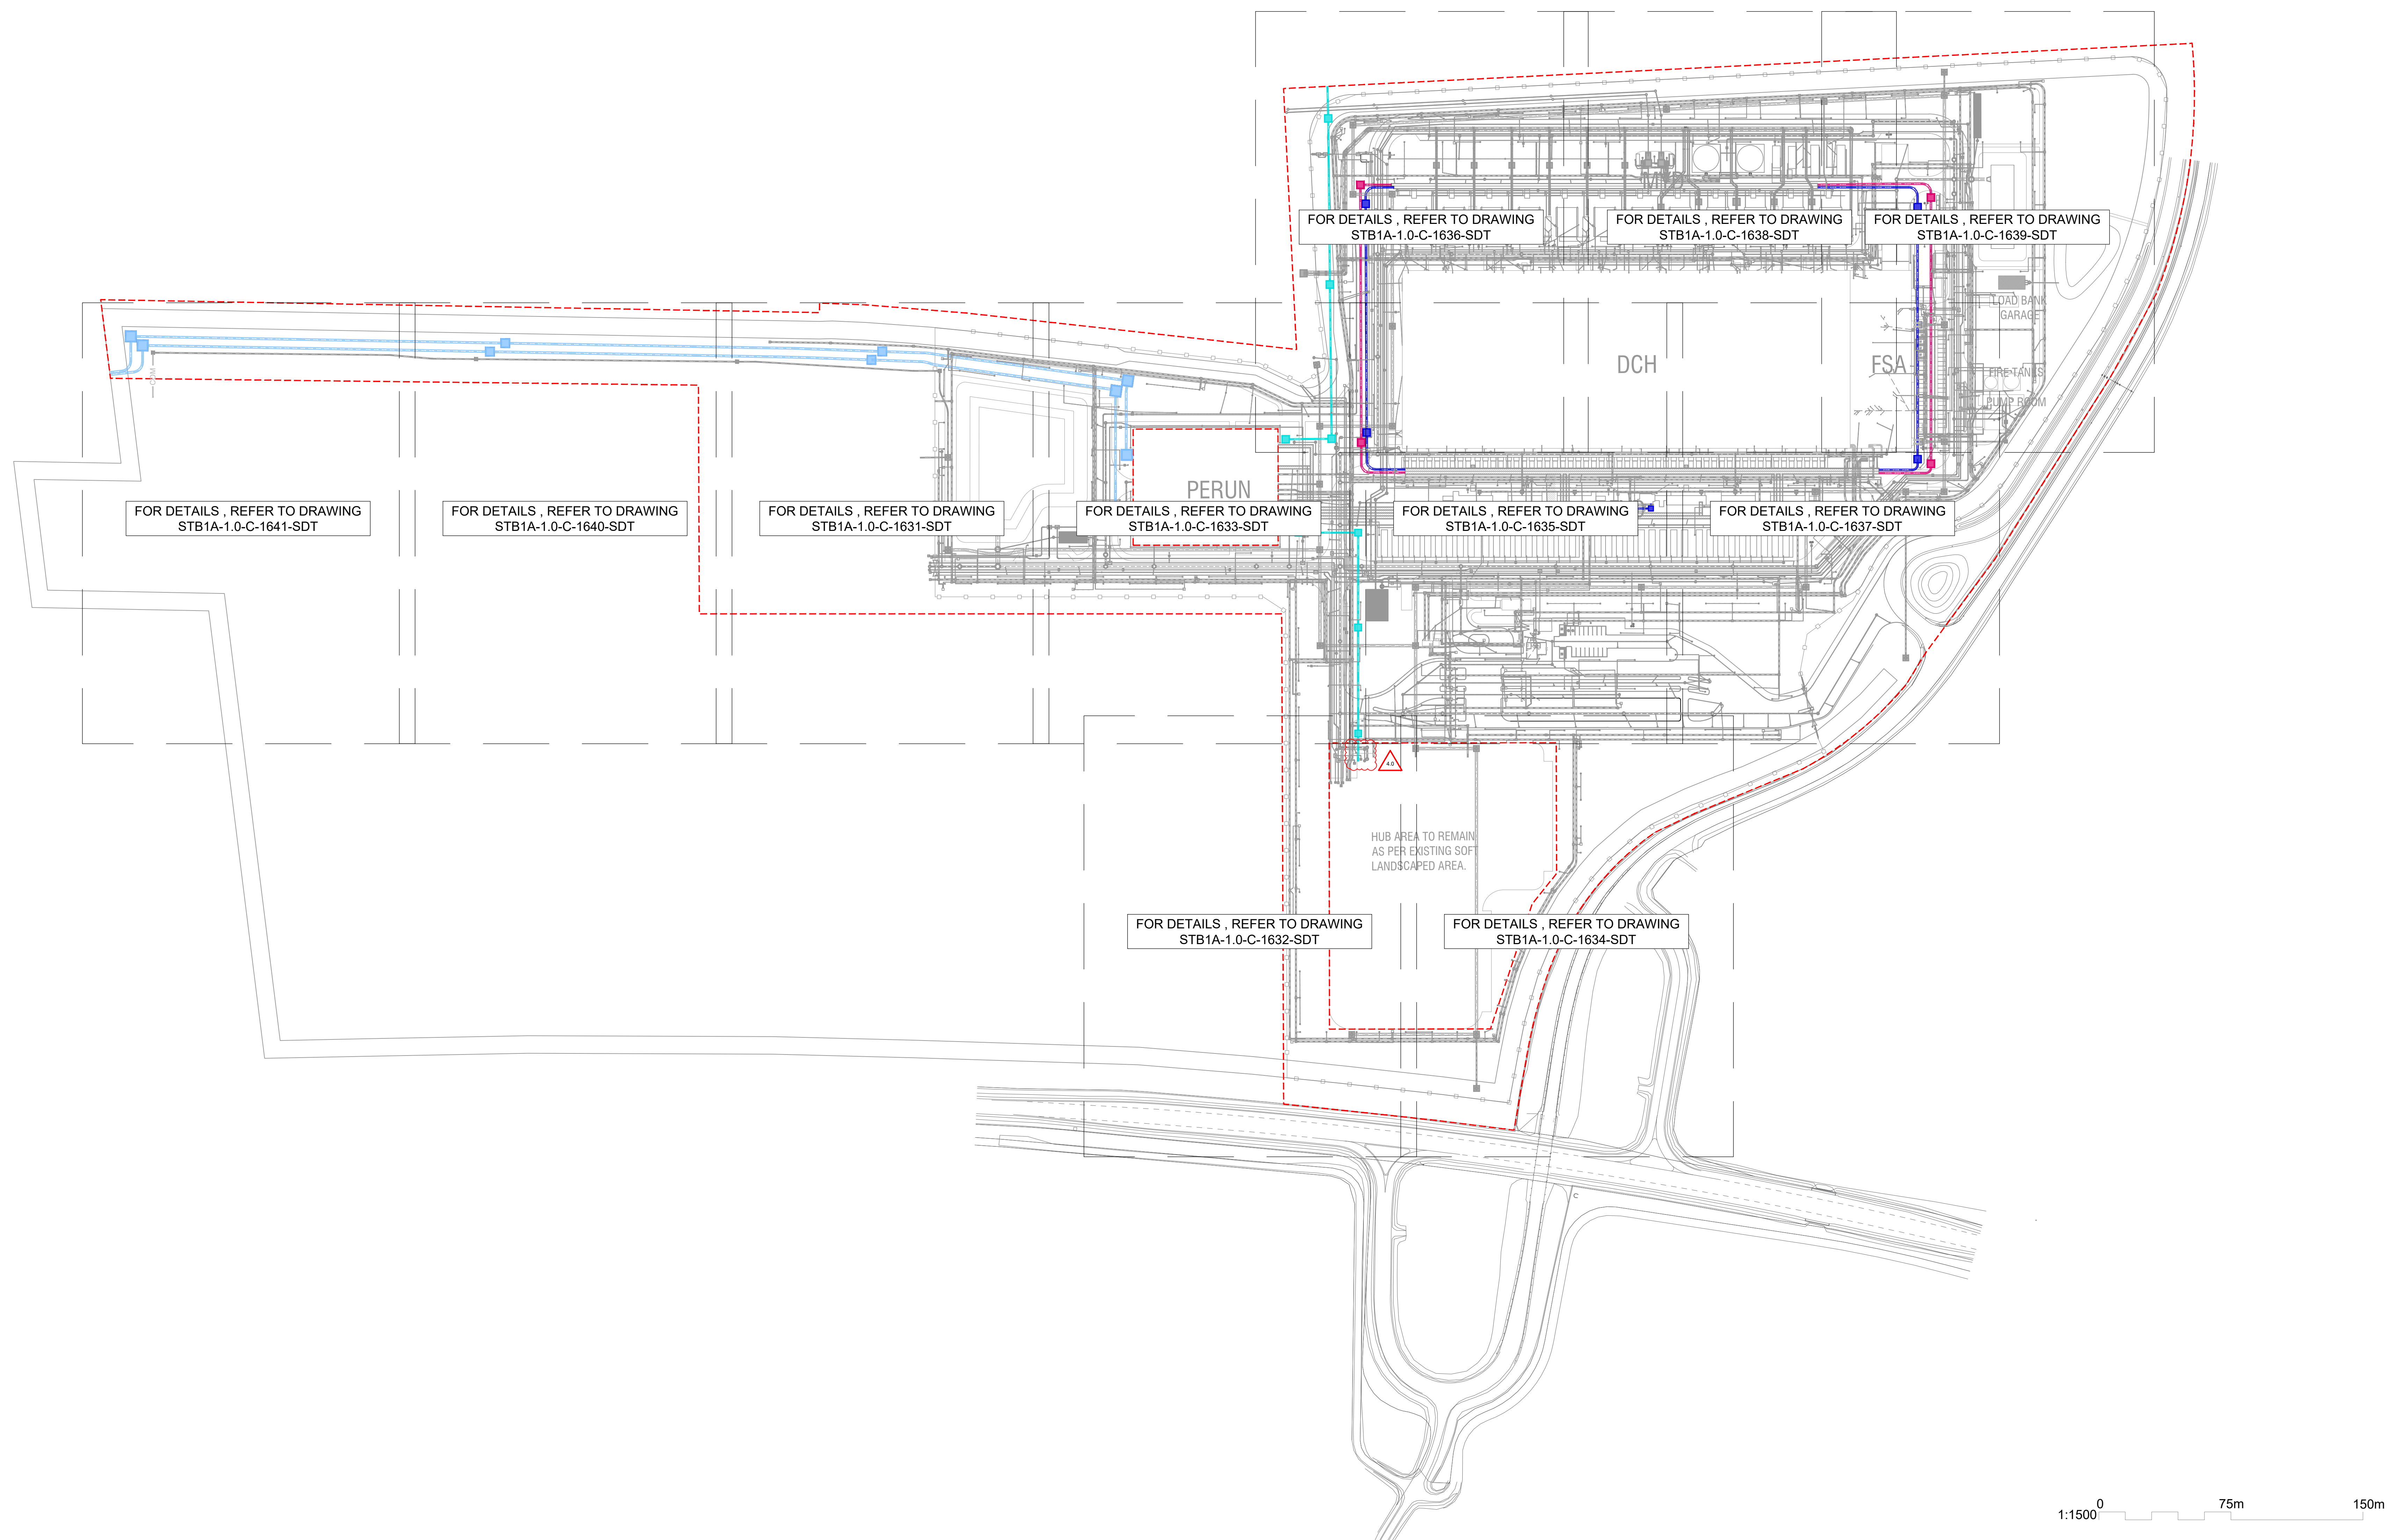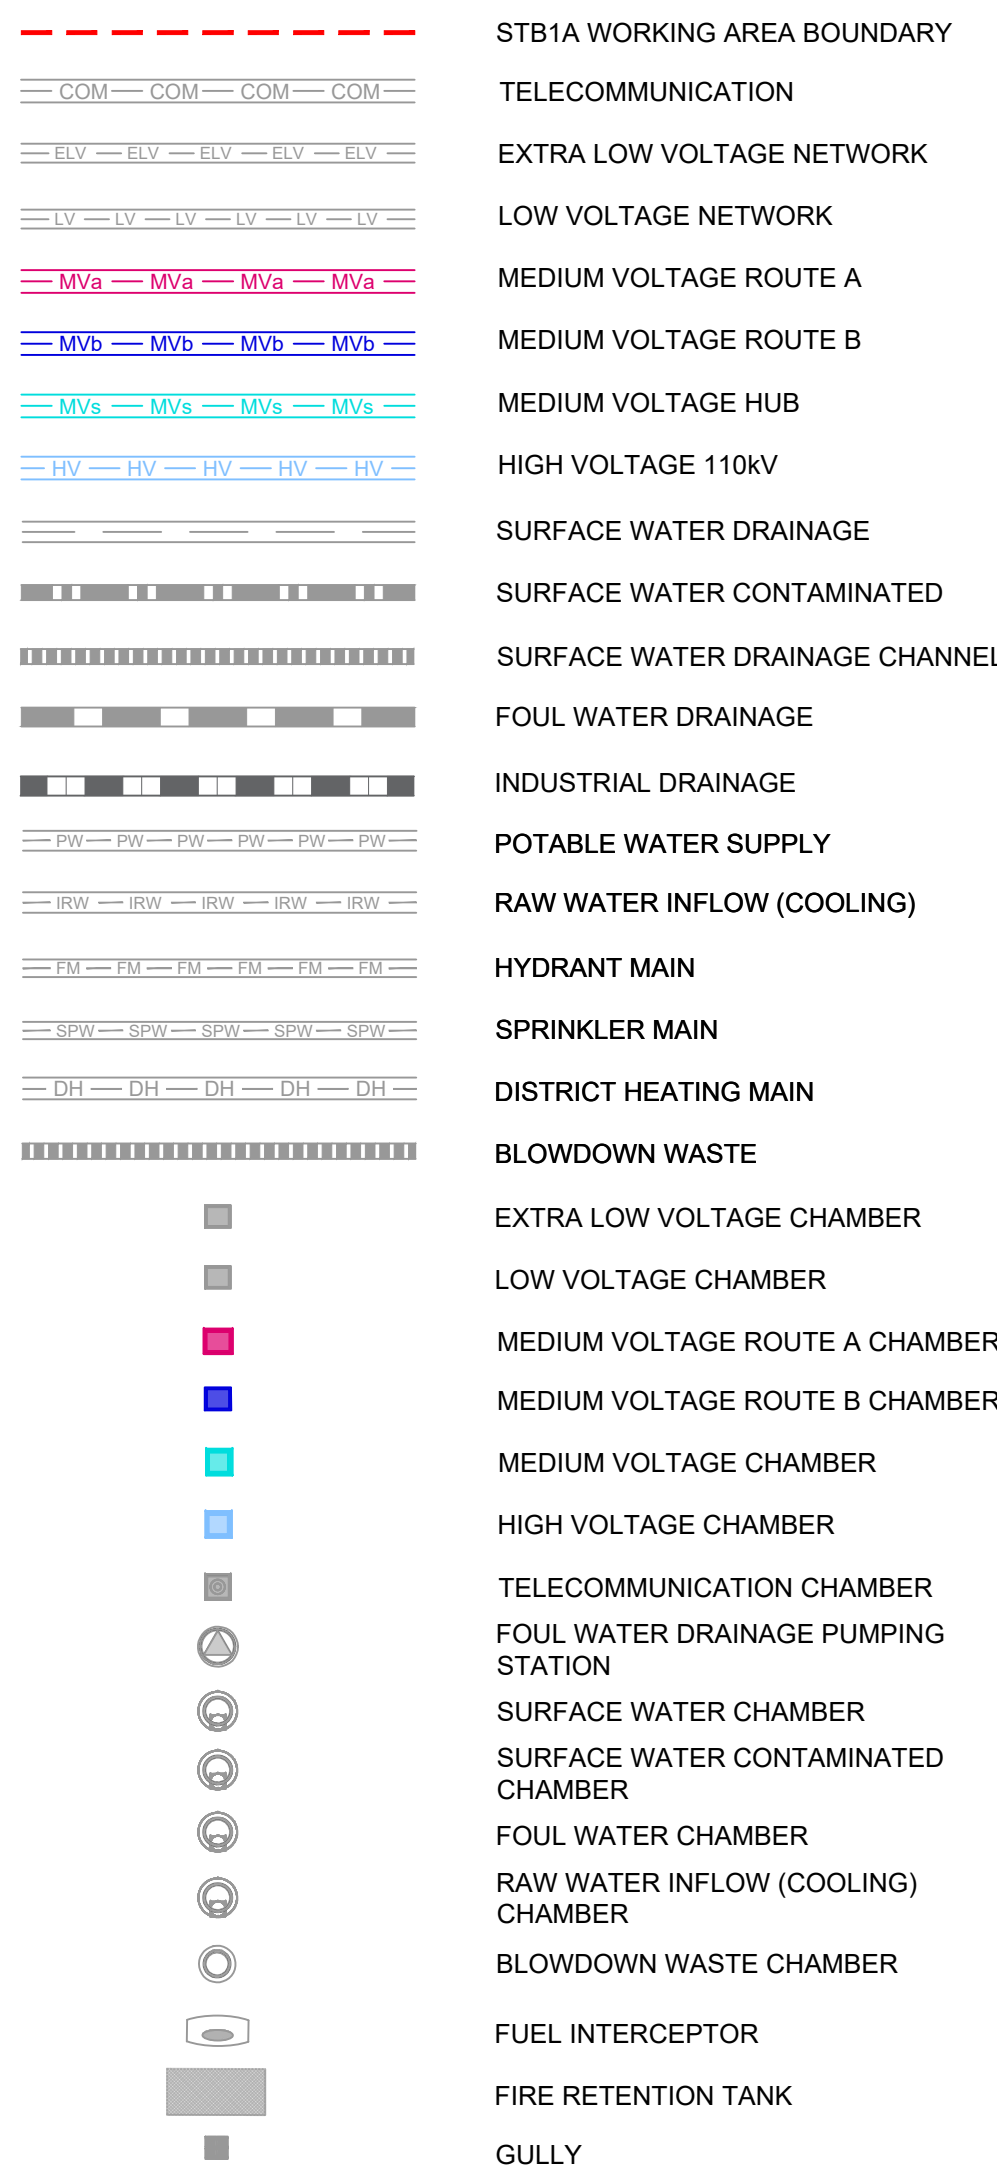

ARCHITECTURE:

ARC:MC
140-142 St. John Street,
London, EC1V 4UB
United Kingdom
t: +44 (0) 203 411 2571
e: info@arcmc.co.uk


INFRASTRUCTURE / CIVILS:

SWECO
Eldon House
2-3 Eldon Street
London
EC2M 7LS
+44 (0) 20 3002 1210
e: www.sweco.co.uk

MEP:

Black & White Engineering
69 Wilson Street,
London, EC2A 2BB
United Kingdom
t: +44 (0) 207 683 7166
e: londonenq@bw-engineering.com

STB1A - PUF - IFC FINAL ISSUE
(ISSUE FOR CONTRACT)
2026-01-23

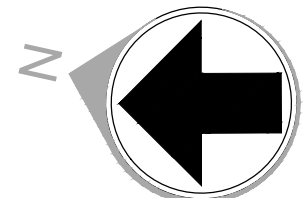

REVISIONS		
NO.	DATE	DESCRIPTION
0.1	16/01/2025	DRAFT IFC ISSUE
0.2	21/02/2025	DRAFT IFC UPDATES
0.3	12/03/2025	DRAFT IFC UPDATES
1.0	11/04/2025	IFC FINAL ISSUE
1.1	30/05/2025	POST IFC DRAFT ISSUE
2.0	04/07/2025	POST IFC FINAL ISSUE
2.1	05/08/2025	POST IFC DRAFT ISSUE
2.2	24/10/2025	POST IFC DRAFT ISSUE
3.0	09/01/2026	POST IFC DRAFT ISSUE
4.0	23/01/2026	POST IFC FINAL ISSUE

Drawn By:	MRP
Approved By:	CM
Design Team:	BW

STB1A

BUCKINGHAM

Project Number: 65212899

Proposed Site Medium and High Voltage Services Layout Overview

Discipline: Civil

Scale: 1:1500 Sheet Size: A0

Sheet Number:

STB1A-1.0-C-1630-SDT

Current Rev: 4.0

Phase: IFC

Native File Format: Civil 3D V.2024