

Disclaimer:
We confirm that calfordseaden LLP has undertaken services relating to coordination of designer's drawings in digital format which includes clash detection. calfordseaden LLP has not attended the site or undertaken site inspection service and therefore the services are desk based only. We provide these drawings as final issue drawings to the Contractor and these drawings include amendments which have been made on the site insofar as such amendments have been communicated to calfordseaden LLP in writing by the Contractor - the Contractor shall verify that these drawings are indeed as built by it on the site.

0
1:250 12.5m 25m

ARCHITECTURE:

ARC:MC
140-142 St. John Street,
London, EC1V 4UB
United Kingdom
t: +44 (0) 203 411 2571
e: info@arcmc.co.uk



INFRASTRUCTURE / CIVILS:

SWECO
Eldon House
2-3 Eldon Street
London
EC2M 7LS
+44 (0) 20 3002 1210
e: www.sweco.co.uk

MEP:

Black & White Engineering
69 Wilson Street,
London, EC2A 2BB
United Kingdom
t: +44 (0) 207 683 7166
e: londoneng@bw-engineering.com

STB1A - PUF - IFC
ISSUED FOR CONSTRUCTION
13/02/2026

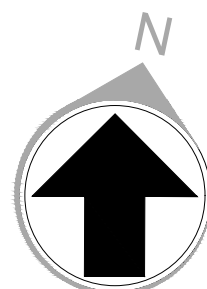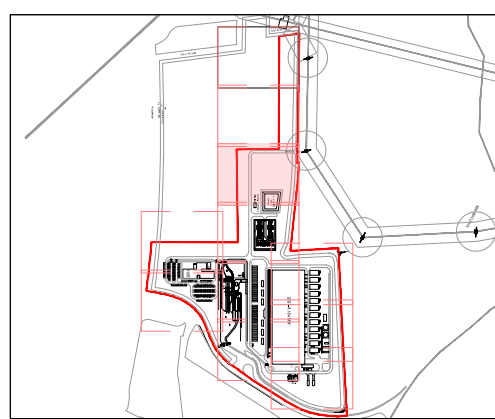

REVISIONS			Drawn By:
NO.	DATE	DESCRIPTION	MP
0.1	18/01/2025	DRAFT IFC ISSUE	Approved By:
0.2	21/02/2025	DRAFT IFC UPDATES	PD
0.3	12/03/2025	DRAFT IFC UPDATES	Design Team:
1.0	11/04/2025	IFC FINAL ISSUE	BW
2.0	04/07/2025	POST IFC FINAL ISSUE	
3.0	09/02/2026	IFC ISSUE - CONSTRUCTION	
4.0	13/02/2026	IFC ISSUE - CONSTRUCTION	

STB1A

BUCKINGHAM

Project Number: 65212899

Proposed Site Fibre Layout
Sheet 1

Discipline: Civil

Scale: 1:250

Sheet Size: A0

Sheet Number:

STB1A-1.0-C-1611-SDT

Current Rev: 4.0

Phase: IFC

Drawing Name: STB1A-1.0-C-1611-SDT.dwg

Native File Format: Civil 3D V.2024

NOTES:

- ALL LEVELS ARE IN METRES ABOVE DATUM UNLESS STATED OTHERWISE.
- DO NOT SCALE FROM THIS DRAWING. ALL DIMENSIONS INDICATED ARE IN METRES UNLESS OTHERWISE STATED. VALIDATE ALL MEASUREMENTS ON SITE.
- ANY DISCREPANCIES BETWEEN THE DRAWINGS AND OTHER DOCUMENTS SHOULD BE BROUGHT TO THE ATTENTION OF THE ENGINEER.
- THIS DRAWING IS NOT AN INSTALLATION DRAWING. IT IS THE CONTRACTORS RESPONSIBILITY TO MAKE FINAL COORDINATED INSTALLATION SHOP DRAWINGS.
- THE CONTENTS OF THIS DRAWING SHALL BE READ IN CONJUNCTION WITH THE CURRENT REVISIONS OF ARCHITECTURAL, CIVIL, STRUCTURAL, MECHANICAL, ELECTRICAL, SECURITY, TELECOMS DRAWINGS AND ALL RELEVANT SECTIONS OF THE SPECIFICATIONS.

ADDITIONAL NOTES:

- FOR REFERENCE OF DETAILS, PLEASE SEE SHEET STB1A-1.0-C-8610-SDT, STB1A-1.0-C-8611-SDT AND STB1A-1.0-C-8612.
- ALL SECONDARY TELECOMMUNICATION DUCTS TO BE 50MM ID/ 63MM OD DUCTS.

LEGEND

---	STB1A WORKING AREA BOUNDARY
COM --- COM --- COM --- COM ---	TELECOMMUNICATION
ELV --- ELV --- ELV --- ELV ---	EXTRA LOW VOLTAGE NETWORK
LV --- LV --- LV --- LV ---	LOW VOLTAGE NETWORK
MVA --- MVA --- MVA --- MVA ---	MEDIUM VOLTAGE ROUTE A
MVB --- MVB --- MVB --- MVB ---	MEDIUM VOLTAGE ROUTE B
MVA --- MVB --- MVA --- MVB ---	MEDIUM VOLTAGE HUB
HV --- HV --- HV --- HV ---	HIGH VOLTAGE 110kV
---	SURFACE WATER DRAINAGE
---	SURFACE WATER CONTAMINATED
---	SURFACE WATER DRAINAGE CHANNEL
---	FOUL WATER DRAINAGE
---	INDUSTRIAL DRAINAGE
PW --- PW --- PW --- PW --- PW ---	POTABLE WATER SUPPLY
RAW --- RAW --- RAW --- RAW --- RAW ---	RAW WATER INFLOW (COOLING)
PM --- PM --- PM --- PM --- PM ---	HYDRANT MAIN
SPW --- SPW --- SPW --- SPW --- SPW ---	SPRINKLER MAIN
DH --- DH --- DH --- DH --- DH ---	DISTRICT HEATING MAIN
---	BLOWDOWN WASTE
---	SECONDARY LV DUCTING ROUTE
---	SECONDARY ELV DUCTING ROUTE
COM --- COM --- COM --- COM ---	SECONDARY TELECOMMUNICATION ROUTE
■	EXTRA LOW VOLTAGE CHAMBER
■	LOW VOLTAGE CHAMBER
■	MEDIUM VOLTAGE ROUTE A CHAMBER
■	MEDIUM VOLTAGE ROUTE B CHAMBER
■	SECURITY MEDIUM VOLTAGE CHAMBER
■	HIGH VOLTAGE CHAMBER
■	TELECOMMUNICATION CHAMBER
■	FOUL WATER DRAINAGE PUMPING STATION
■	SURFACE WATER CHAMBER
■	SURFACE WATER CONTAMINATED CHAMBER
■	FOUL WATER CHAMBER
■	RAW WATER INFLOW (COOLING) CHAMBER
■	BLOWDOWN WASTE CHAMBER
■	FUEL INTERCEPTOR
■	FIRE RETENTION TANK
■	GULLY