


- NOTES:
- DO NOT SCALE FROM THIS DRAWING. ALL DIMENSIONS INDICATED ARE IN METRES UNLESS OTHERWISE STATED. VALIDATE ALL MEASUREMENTS ON SITE.
 - ANY DISCREPANCIES BETWEEN THE DRAWINGS AND OTHER DOCUMENTS SHOULD BE BROUGHT TO THE ATTENTION OF THE ENGINEER.
 - THIS DRAWING IS NOT AN INSTALLATION DRAWING. IT IS THE CONTRACTORS RESPONSIBILITY TO MAKE FINAL COORDINATED INSTALLATION SHOP DRAWINGS.
 - THE CONTENTS OF THIS DRAWING SHALL BE READ IN CONJUNCTION WITH THE CURRENT REVISIONS OF ARCHITECTURAL, CIVIL, STRUCTURAL, MECHANICAL, ELECTRICAL, SECURITY, TELECOMS DRAWINGS AND ALL RELEVANT SECTIONS OF THE SPECIFICATIONS.

FOUL WATER STRUCTURE SCHEDULE											
MANHOLE NAME	EASTING (m)	NORTHING (m)	COVER LEVEL (m)	SUMP LEVEL (m)	DEPTH (m)	INLET PIPE (mmØ)	INLET PIPE INVERT LEVEL (m)	OUTLET PIPE (mmØ)	OUTLET PIPE INVERT LEVEL (m)	MANHOLE SIZE (mm)	NOTES
FW Pumping Station 1	83516.481	332043.897	309.291	304.648	4.643	225 225	304.648 304.684			1800	
FW Pumping Station 2	83445.413	332001.247	308.927	303.626	5.301	225	303.626	225	305.760	1800	
FW1	83346.616	331989.002	309.103	306.522	2.581			150	306.533	1200	
FW3	83659.032	331717.766	308.944	307.105	1.839	150 150	307.705 307.705	150	307.705	1200	
FW4	83723.795	331732.431	309.050	307.263	1.787	150 150	307.263 307.274	150	307.263	1200	
FW5	83714.517	331773.404	308.922	306.853	2.070	225	306.853	225	306.853	1200	
FW6	83685.869	331766.900	309.208	306.706	2.502	225	306.720	225	306.706	1200	
FW7	83672.610	331824.616	309.093	306.410	2.683	225	306.410	225	306.410	1200	
FW8	83667.319	331847.995	309.093	306.290	2.803	225 105	306.290 307.285	225	306.290	1200	
FW9	83650.915	331920.492	309.093	305.919	3.174	225	305.919	225	305.919	1200	
FW10	83640.564	331966.238	309.093	305.683	3.410	225 105	305.683 306.883	225	305.683	1200	
FW11	83623.836	332040.165	308.916	305.304	3.612	225	305.304 305.429	225	305.304	1200	
FW12	83565.528	332026.961	308.923	305.005	3.918	225	305.005	225	305.005	1200	
FW15	83397.837	332254.052	308.376	306.781	1.595			225	306.781	1200	REQUIRE LOCKABLE LIDS
FW16	83422.135	332146.769	309.125	306.152	2.973	225	306.152	225	306.152	1200	
FW17	83448.882	332028.582	308.891	305.215	3.676	225 225	305.215 305.215	225	305.215	1200	
FW18	83440.390	331910.550	309.780	307.454	2.326	105	307.454	150	307.454	1200	
FW19	83402.644	332018.111	308.911	305.689	3.222	150	305.762	225	305.689	1200	
FW20	83467.159	331916.631	309.018	306.155	2.863	150 225	306.170 306.155	225	306.155	1200	
FW21	83565.377	332054.960	308.903	307.149	1.754	225	307.149	225	307.149	1200	
FW25	83654.137	331739.308	309.122	308.065	1.057	100	308.114	150	308.065	1200	
FW26	83696.212	331712.192	308.752	307.551	1.201	150	307.551	150	307.551	1200	
FW29	83442.075	332027.039	308.894	305.261	3.633	225 225	305.366 305.261	225	305.266	1200	
FW30	83502.946	331759.117	309.242	307.449	1.792	225	307.449	225	307.449	1200	
FW31	83524.147	331749.931	308.911	307.657	1.254	150	307.865	225	307.657	1200	
FW33	83349.324	332006.038	308.834	306.309	2.525	150	306.309	150	306.309	1200	
FW34	83522.540	332017.226	308.929	304.785	4.144	225	304.785	225	304.785	1200	
FW36	83453.112	331978.459	308.868	305.654	3.214	225	305.654	225	305.654	1200	
FW37	83447.811	332001.794	308.888	305.465	3.422	225 225	305.465 305.741	225	305.465	1200	
FW39	83716.481	331784.731	309.037	306.967	2.069	150	307.042	225	306.967	1200	
FW41	83414.079	332182.349	309.125	306.361	2.764	225	306.361	225	306.361	1200	
FW42	83487.282	331826.060	308.996	306.873	2.124	225	306.873	225	306.873	1200	
FW43	83495.861	331790.301	308.987	307.178	1.809	225	307.178	225	307.178	1200	SHUT-OFF VALVE CHAMBER
FW44	83478.292	331867.632	309.006	306.552	2.454	225	306.552	225	306.552	1200	
FW45	83352.862	331990.417	309.105	306.469	2.636	150	306.469	150	306.469	1200	
FW46	83516.730	332044.406	309.246	307.466	1.779					1200	VALVE CHAMBER
FW47	83563.559	332067.620	308.976	307.000	1.976	225	307.000			1200	EXISTING CHAMBER
FW48	83703.426	331719.872	308.763	307.481	1.282	150 150	307.481 307.496	150	307.481	1200	
FW49	83725.506	331724.866	308.780	307.326	1.454	150	307.326	150	307.326	1200	
FW50	83679.843	332051.455	308.944	306.383	2.561	100	306.382	100	306.382	1200	
FW51	83637.233	332041.806	308.949	305.655	3.294	100	305.654	100	305.654	1200	
FW52	83524.265	332045.657	309.091	307.425	1.666			225	307.430	1200	RISING MAIN DISCHARGE CHAMBER
FW53	83435.509	332087.676	309.125	305.684	3.441	225	305.684	225	305.684	1200	
FWIC1	83631.669	331680.837	309.174	308.128	1.046	150 150	308.128 308.128	150	308.128	600	INSPECTION CHAMBER
FWIC2	83609.379	331729.144	309.121	308.228	0.893	150	308.231	150	308.231	600	INSPECTION CHAMBER
FWIC3	83614.251	331707.626	308.910	308.010	0.900	150	308.010	150	308.010	600	INSPECTION CHAMBER
FWIC4	83652.402	331702.278	308.838	307.850	0.988	150	307.850	150	307.850	600	INSPECTION CHAMBER
FWIC5	83627.932	331697.309	308.813	308.016	0.797	150 150	308.016 308.016	150	308.016	600	INSPECTION CHAMBER
FWIC6	83529.667	331756.535	308.658	307.972	0.686			150	307.983	600	INSPECTION CHAMBER

OIL INTERCEPTOR SCHEDULE										
MANHOLE NAME	EASTING (m)	NORTHING (m)	COVER LEVEL (m)	SUMP LEVEL (m)	DEPTH (m)	INLET PIPE (mmØ)	INLET PIPE INVERT LEVEL (m)	OUTLET PIPE (mmØ)	OUTLET PIPE INVERT LEVEL (m)	NOTES
Full Retention Separator 1	83496.418	331783.308	309.321	307.225	2.096	225	307.225	225	307.225	
Full Retention Separator 2	83708.134	331720.935	308.767	307.445	1.322	150	307.445	150	307.445	

FOUL WATER STRUCTURE SCHEDULE								
NAME	TYPE	EASTING	NORTHING	COVER LEVEL (m)	SUMP LEVEL (m)	DEPTH (m)	STRUCTURE SIZE (mmØ)	NOTES
SVP30	SOIL VENT PIPE	83632.972	331676.213	309.161	308.224	0.937	150	
SVP31	SOIL VENT PIPE	83630.329	331687.845	309.162	308.057	1.105	150	
SVP32	SOIL VENT PIPE	83428.570	332197.170	309.474	308.587	0.887	100	
SVP33	SOIL VENT PIPE	83431.760	332183.081	309.504	308.504	1.000	100	
SVP34	SOIL VENT PIPE	83683.138	332062.838	308.692	308.588	2.104	100	

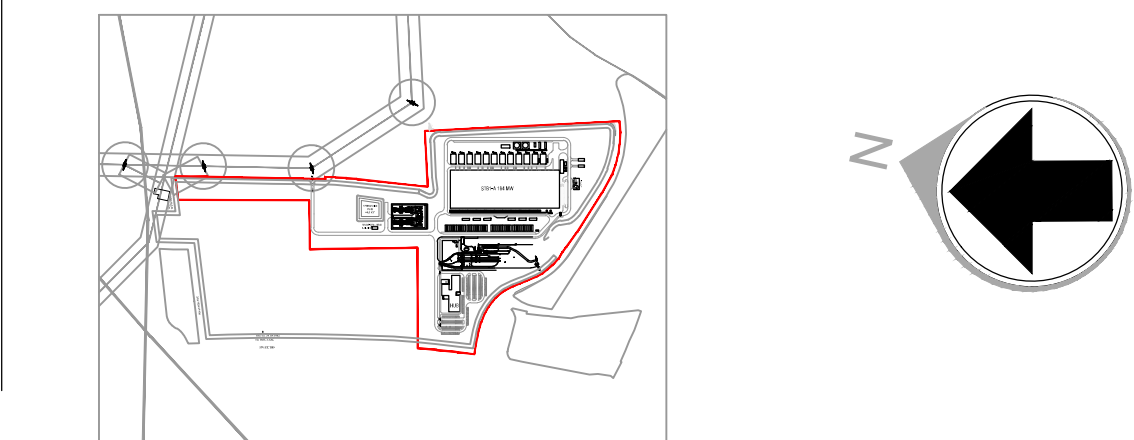

REVISIONS			Drawn By:
NO.	DATE	DESCRIPTION	MRP
0.3	12/03/2025	DRAFT IFC UPDATES	Approved By:
1.0	11/04/2025	IFC FINAL ISSUE	CM
1.1	30/05/2025	POST IFC DRAFT ISSUE	Design Team:
2.0	04/07/2025	POST IFC FINAL ISSUE	BW
2.1	24/10/2025	POST IFC DRAFT ISSUE	
3.0	07/11/2025	POST IFC FINAL ISSUE	
4.0	09/01/2026	POST IFC DRAFT ISSUE	
5.0	23/01/2026	POST IFC FINAL ISSUE	
6.0	13/02/2026	POST IFC FINAL ISSUE	

STB1A

BUCKINGHAM

Project Number: 65212899

Foul Water Schedules

Discipline: Civil

Scale: N.T.S

Sheet Size: A0

Sheet Number:

STB1A-1.0-C-6450-SDT

Current Rev: 6.0

Phase: IFC

Drawing Name: STB1A-1.0-C-6450-SDT.dwg

Native File Format: Civil 3D V.2024

ARCHITECTURE:

ARC:MC
140-142 St. John Street,
London, EC1V 4UB
United Kingdom
t: +44 (0) 203 411 2571
e: info@arcmc.co.uk

INFRASTRUCTURE / CIVILS:

SWECO
Eldon House
2-3 Eldon Street
London,
EC2M 7LS
+44 (0) 20 3002 1210
e: www.sweco.co.uk

MEP:

Black & White Engineering
69 Wilson Street,
London, EC2A 2BB
United Kingdom
t: +44 (0) 207 683 7166
e: londoneng@bw-engineering.com

STB1A - PUF - IFC FINAL ISSUE
(ISSUE FOR CONTRACT)
2026-02-13