



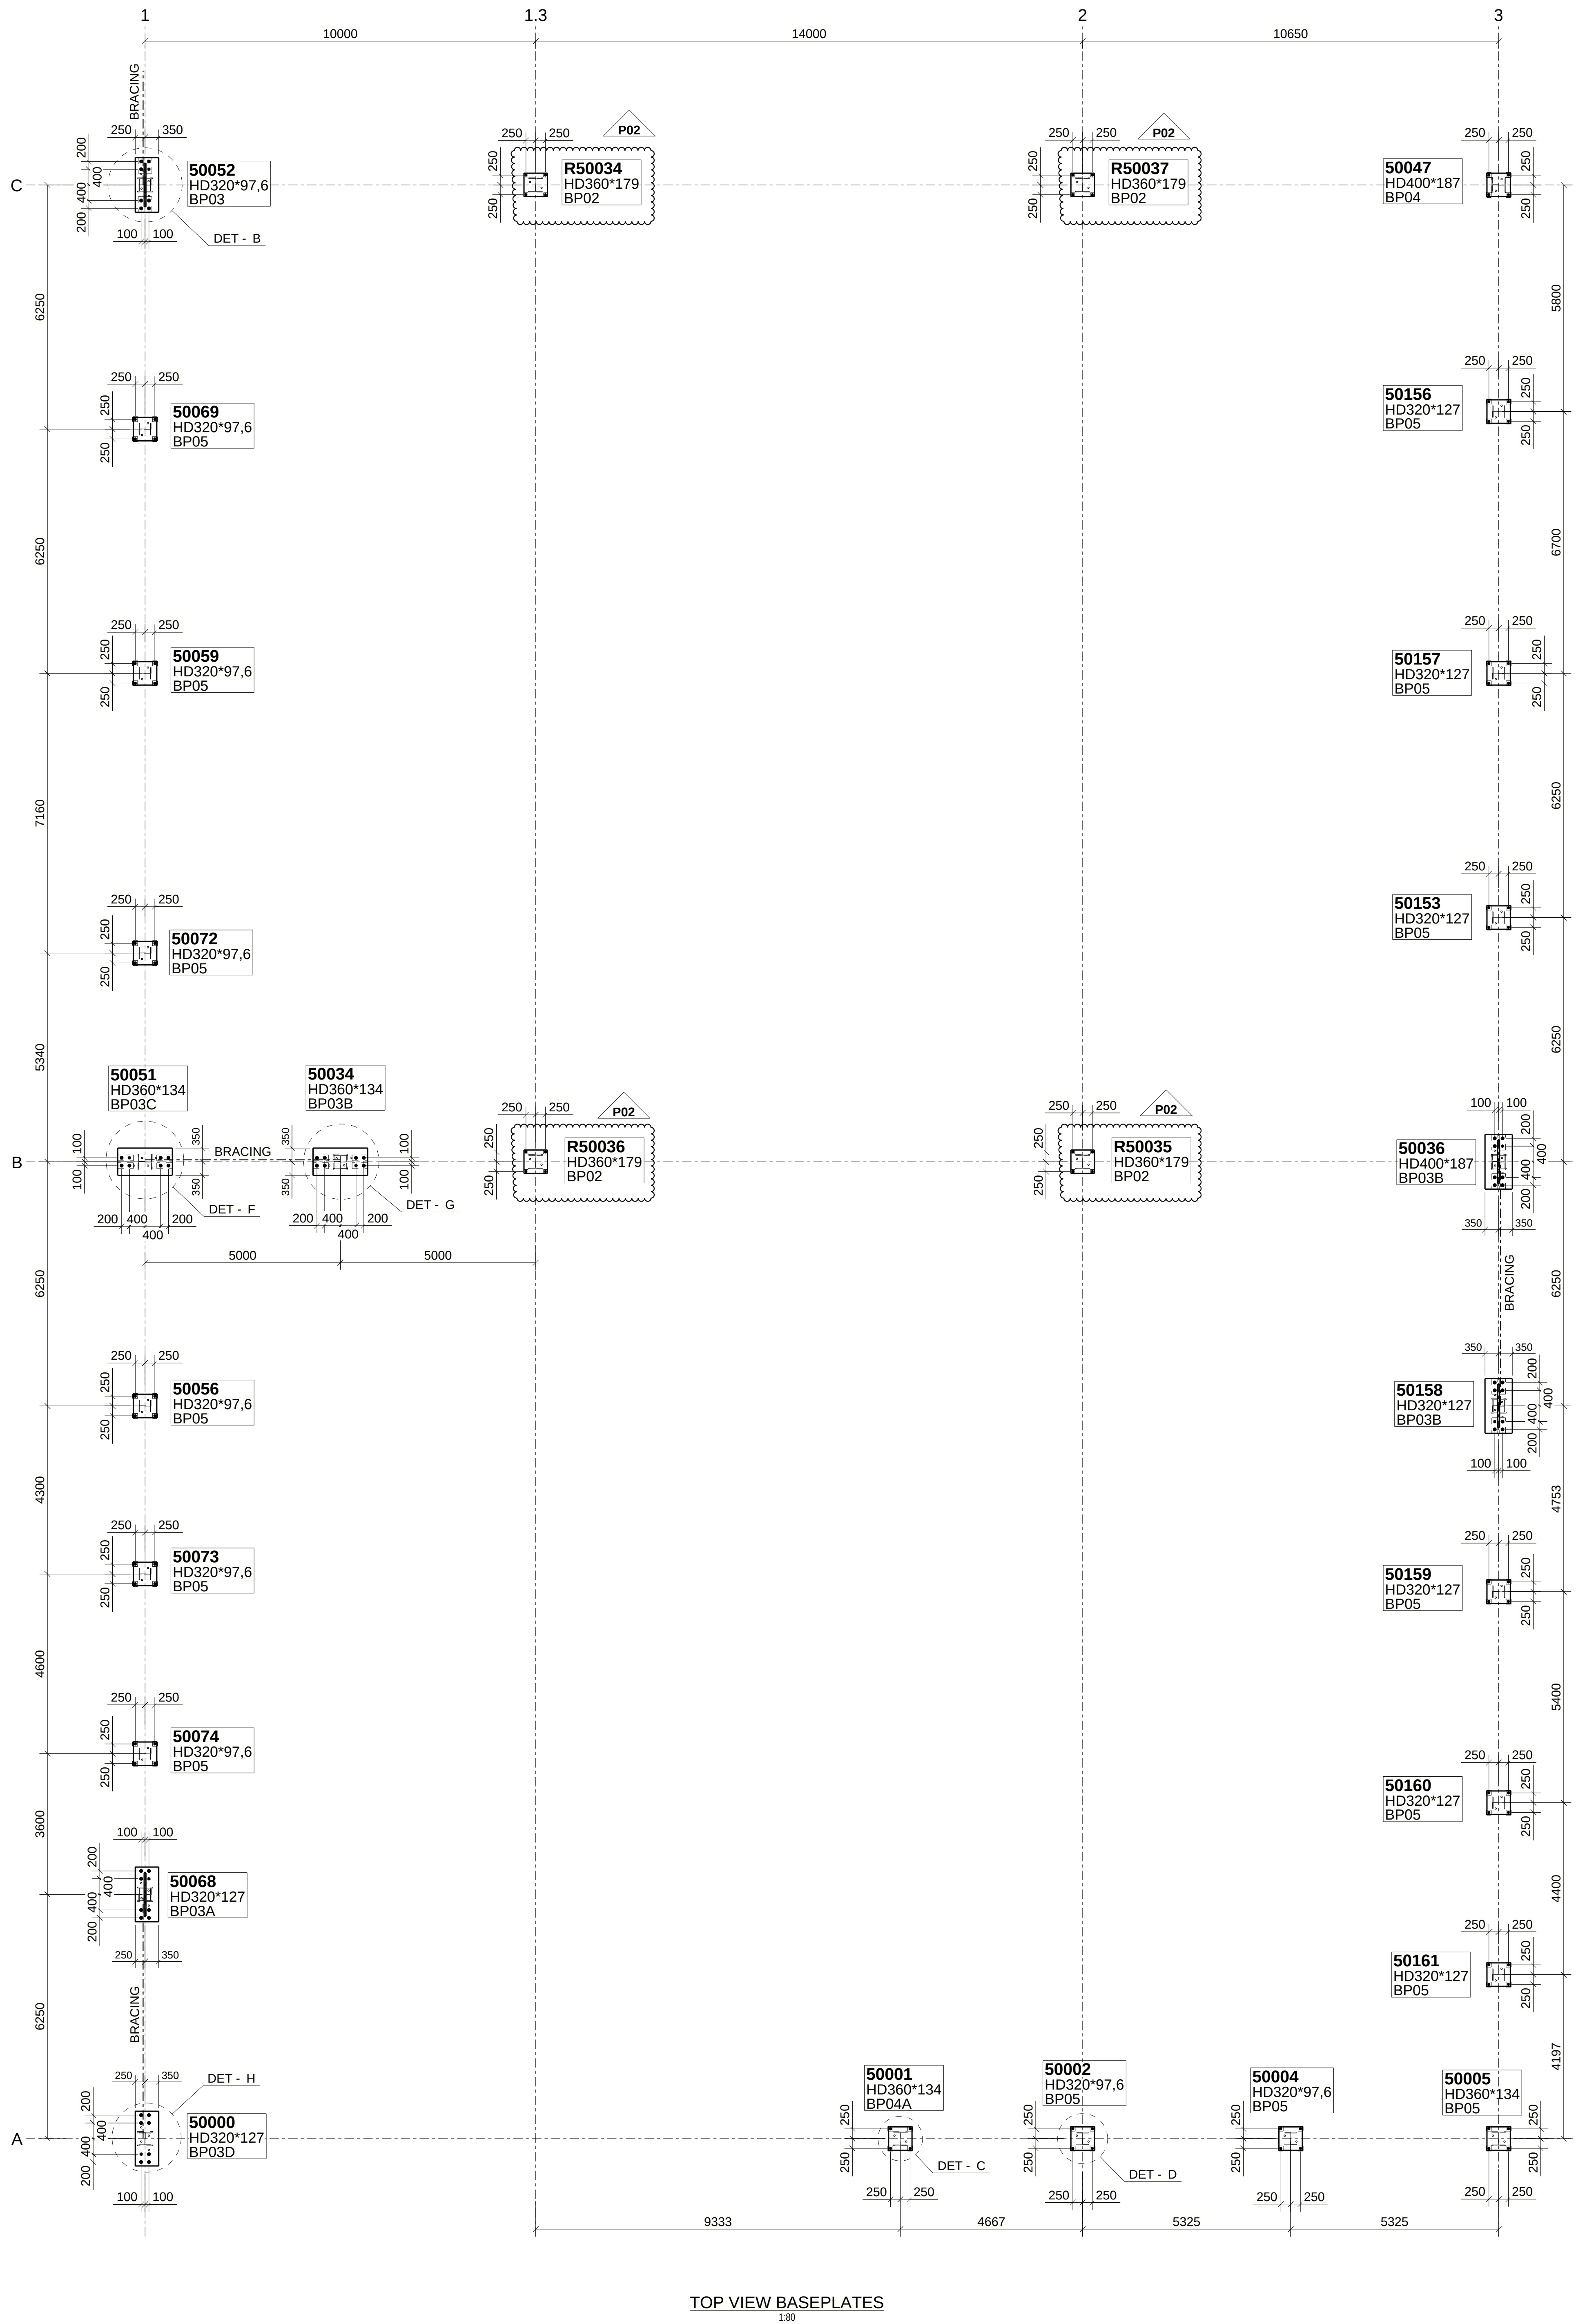


TOP VIEW BASEPLATES
1:50

TYPICAL BASEPLATE DETAILS

NOTE:
FOR ROTATION OF COLUMNS
AND POSITION ANCHORS
SEE TOP VIEW
ALL ANCHORS HOLDING DOWN
BOLTS (CONE NOT SHOWN)

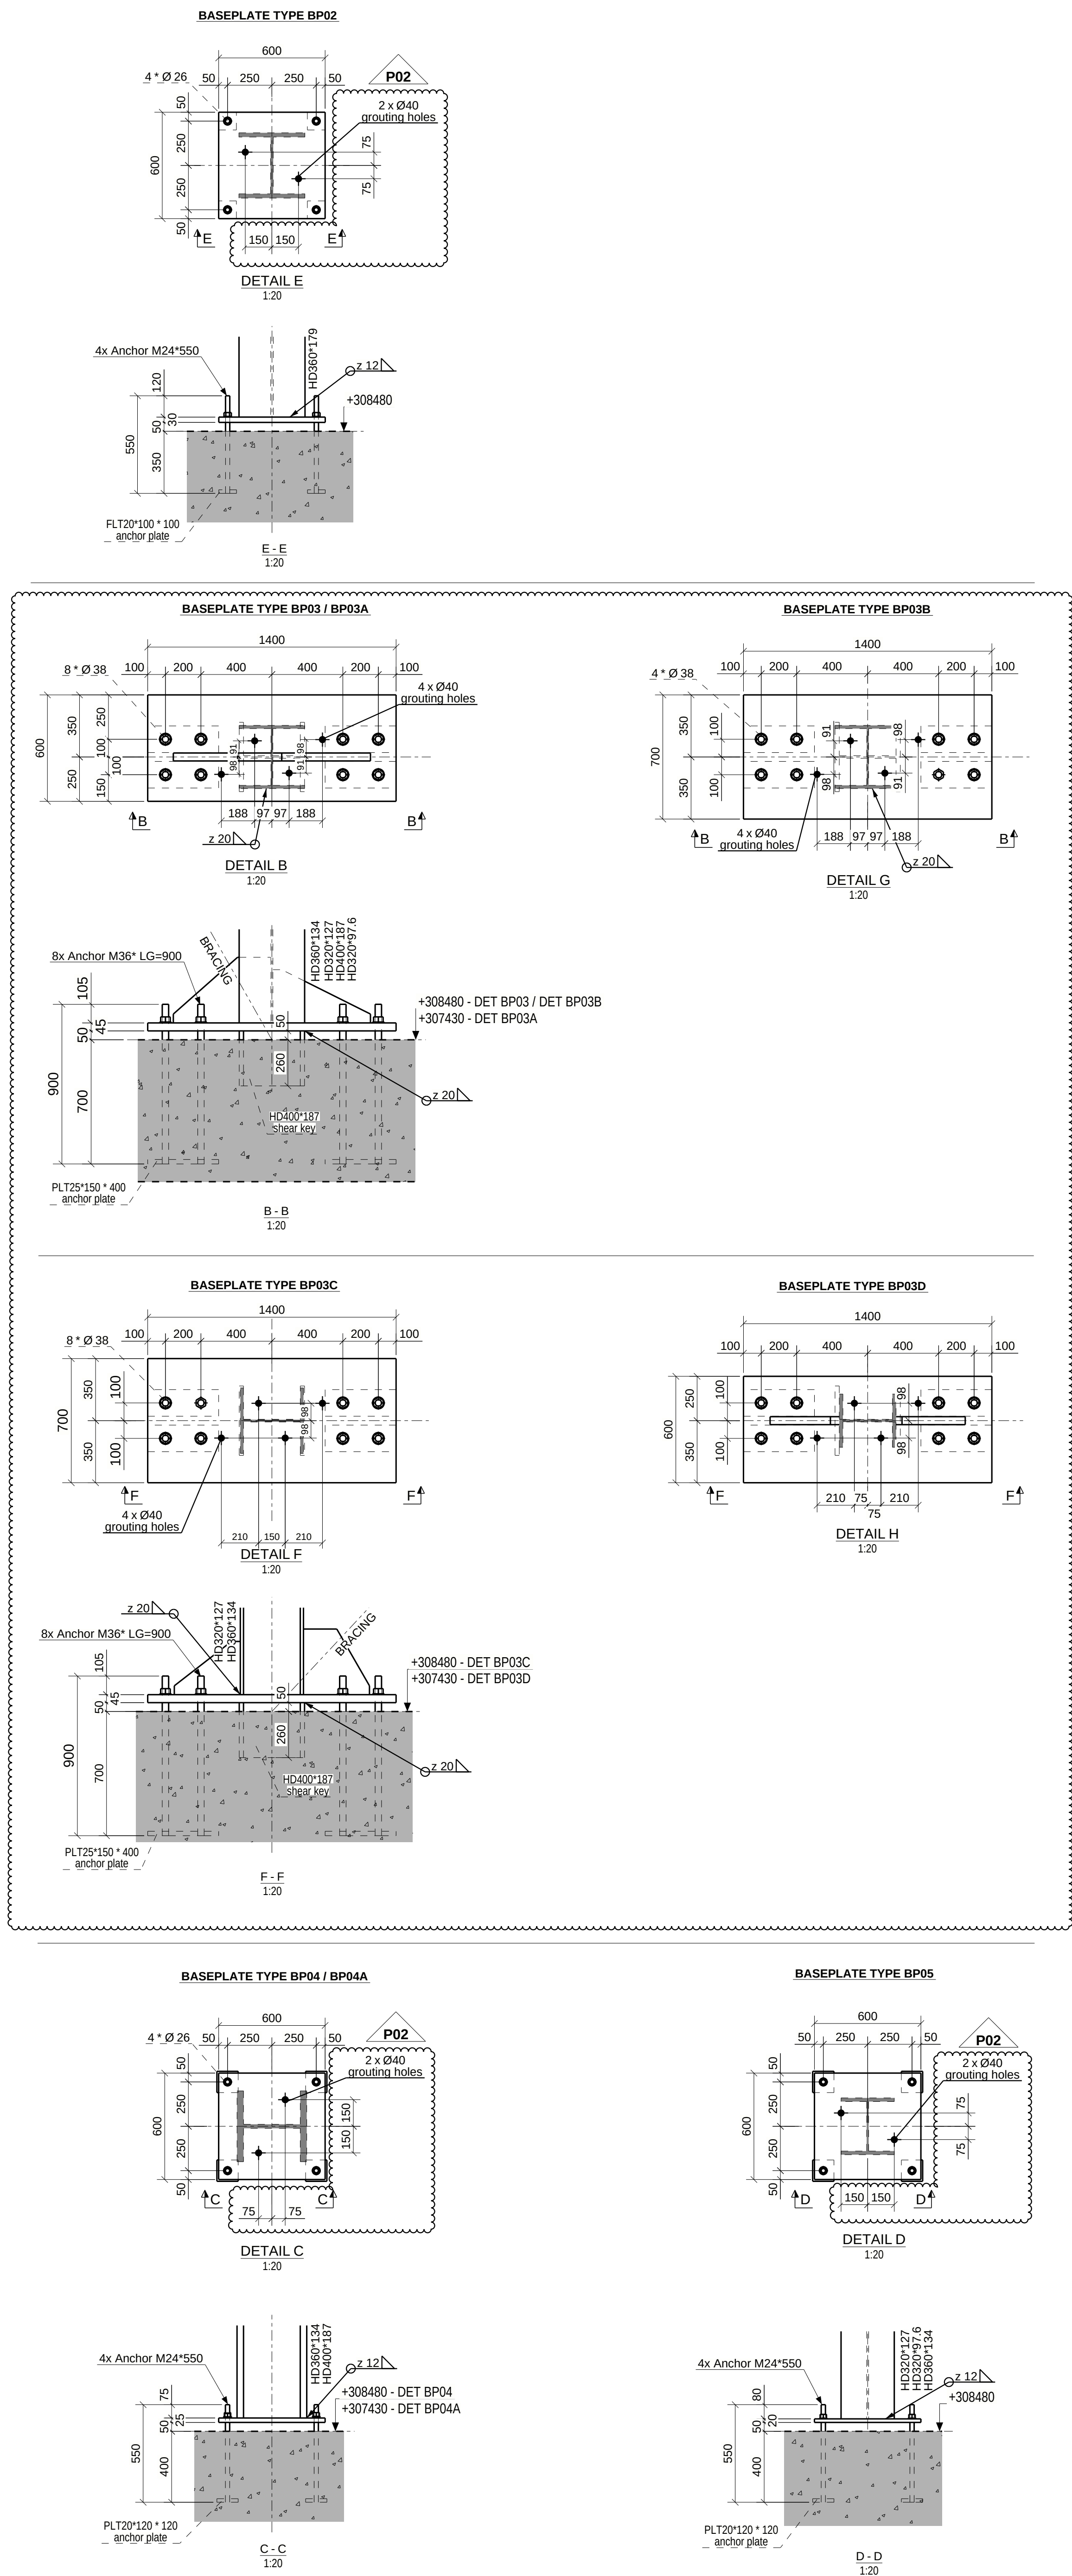

NOTES	
ALL BOLTS GR B.8 GALVANISED U.N.O.	
FABRICATION AND ERECTION TOLERANCES U.N.O. IN ACCORDANCE WITH THE NSSS, PROJECT SPEC AND AGREED PROJECT VALUES.	
⊕ SHOP BOLTS	⊕ SITE BOLTS/HOLES
⊕ C/SUNK NEAR SIDE	⊕ C/SUNK FAR SIDE
▼ DENOTES MEMBER MARK LOCATION.	
COLUMN ORIENTATION MARK U.N.O. IDENTIFIED BY HOLE NEAR BASE OF COLUMN ON SOUTH or WEST FLANGE WHEN VIEWED ON PLAN. (North relevant to local model/drawing), ie.	

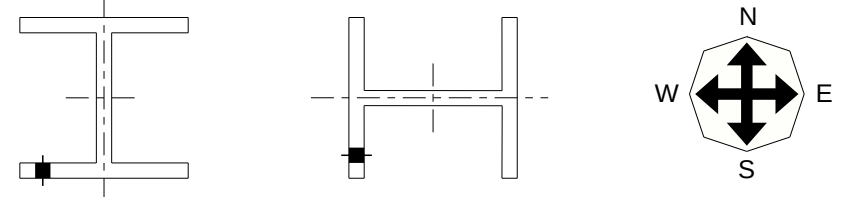

P02

P02	REVISED AS NOTED	SF	EC
P01	FOR APPROVAL	SF	EC
Rev.	Description	Drawn By	Chkd By

Severfield Commercial & Industrial Ltd
Severfield Nuclear & Infrastructure Ltd
Severfield Products & Processing Ltd
www.severfield.com

Client:	TSL
Architect:	
Engineer:	

Project:		STB1A	
Drawing title:		BASEPLATES MAIN COLUMNS FSA GRIDLINE A-C 2	
Dwn By: SF	Chkd by: EC	Apv'd by:	Scale:
Date: 31/10/25	Date: 12/11/25	Date:	1:20 1:80 1:200
SEVERFIELD PROJECT NO: C2147		Status Code:	
Drawing No:		Rev:	
STB1A-2.1-S-1000-FSA		P02	