

NOTES

ALL BOLTS GR 8.8 GALVANISED U.N.O.

FABRICATION AND ERECTION TOLERANCES U.N.O. IN ACCORDANCE WITH THE NSSS, PROJECT SPEC AND AGREED PROJECT VALUES.

◆ SHOP BOLTS

◆ SITE BOLTS/HOLES


◆ C/SUNK NEARSIDE

◆ C/SUNK FAR SIDE

▼ DENOTES MEMBER MARK LOCATION.

COLUMN ORIENTATION MARK U.N.O.










IDENTIFIED BY HOLE NEAR BASE OF COLUMN ON SOUTH or WEST FLANGE WHEN VIEWED ON PLAN. (North relevant to local model/drawing), ie.

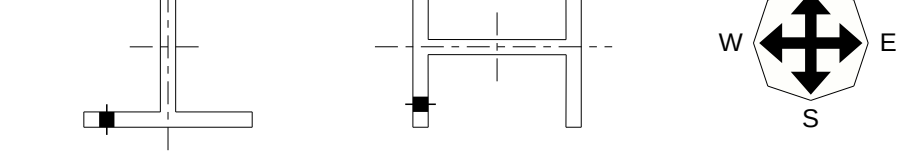

TYPICAL BASEPLATE DETAILS

NOTE:
FOR ROTATION OF COLUMNS
AND POSITION ANCHORS
SEE TOP VIEW

ALL ANCHORS HOLDING DOWN
BOLTS (CONE NOT SHOWN)

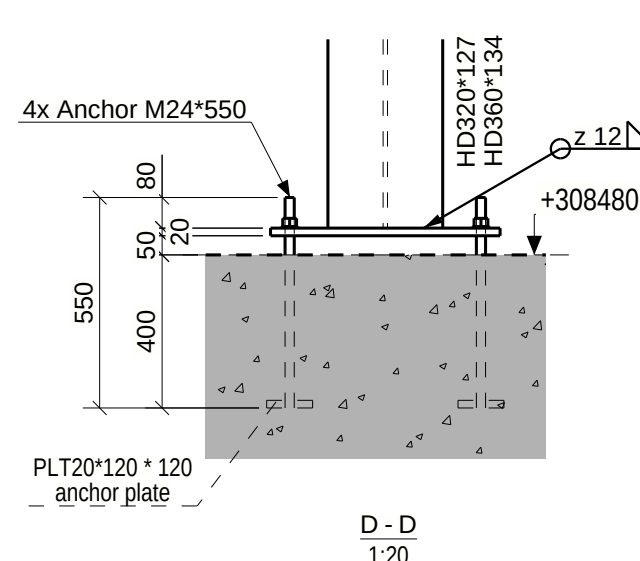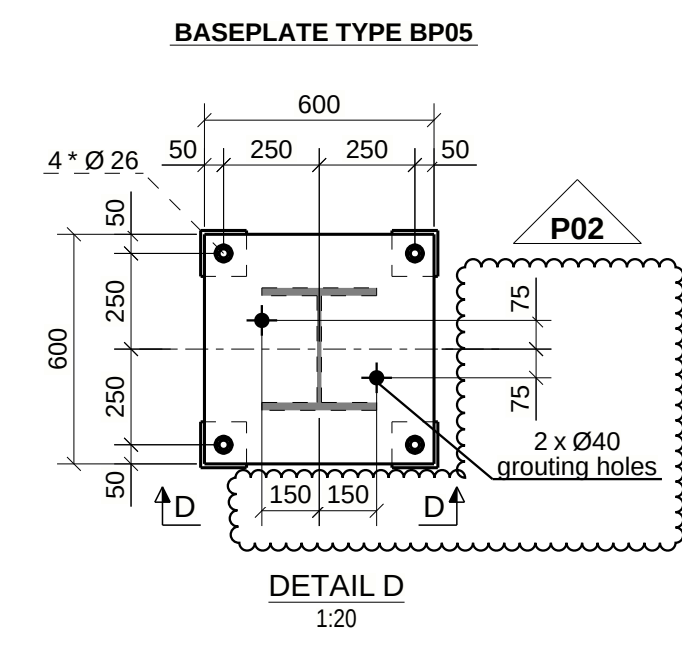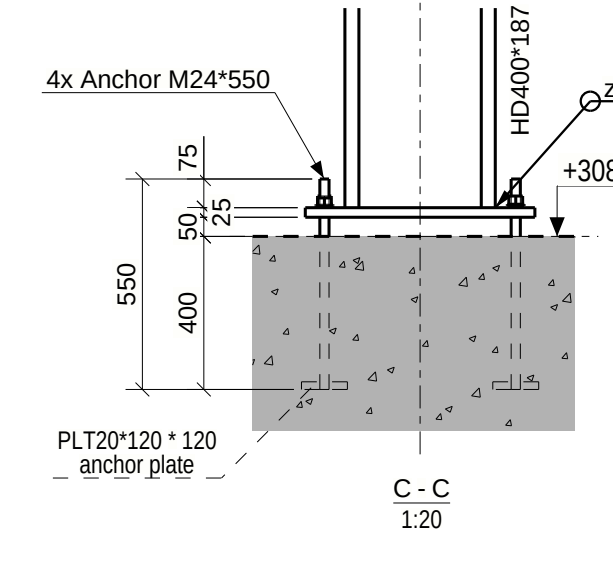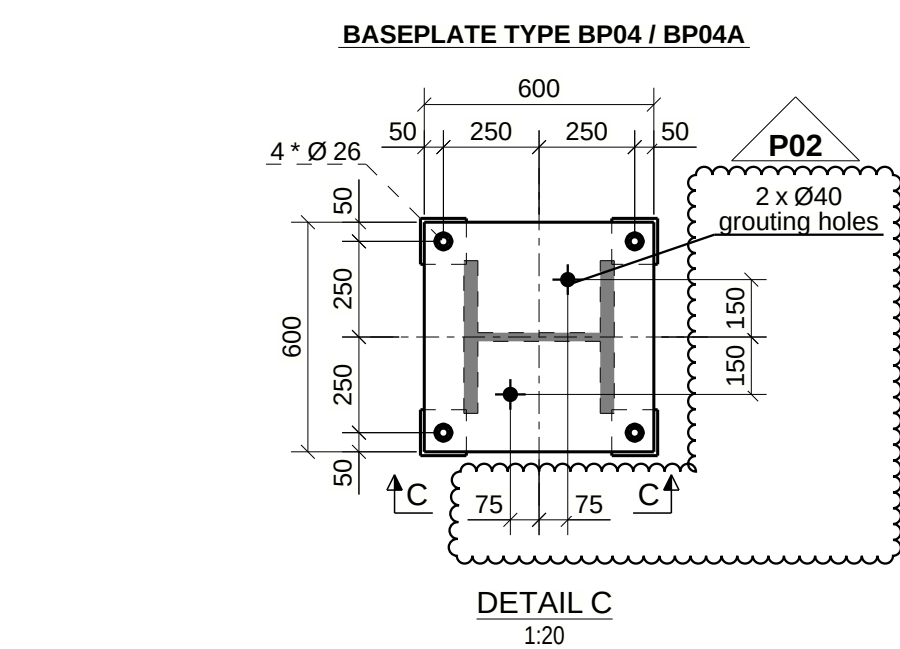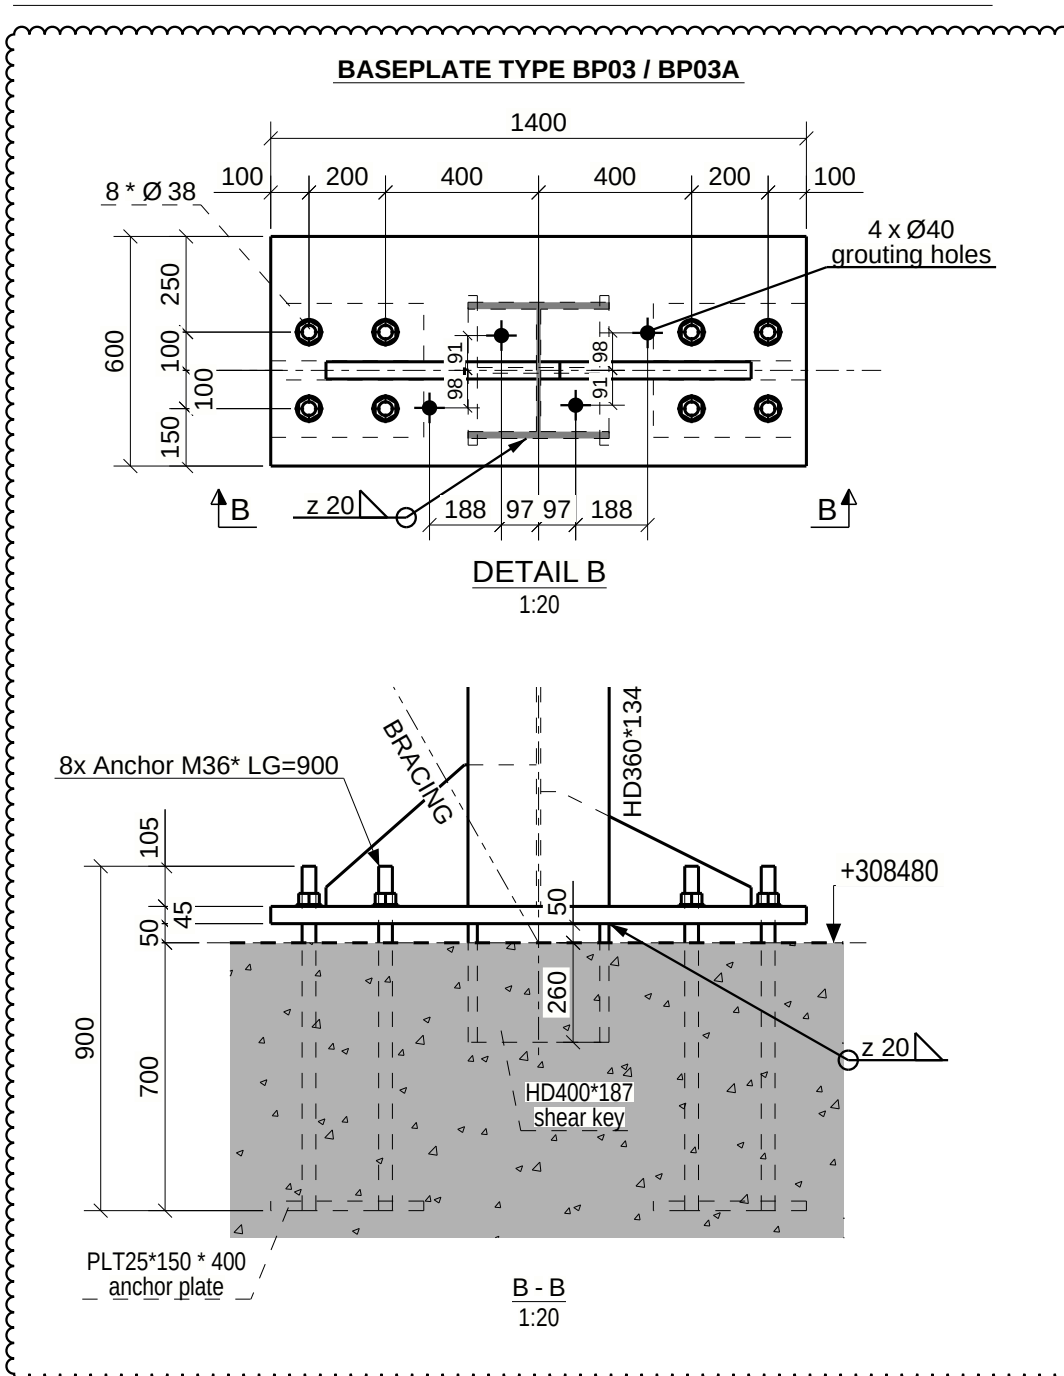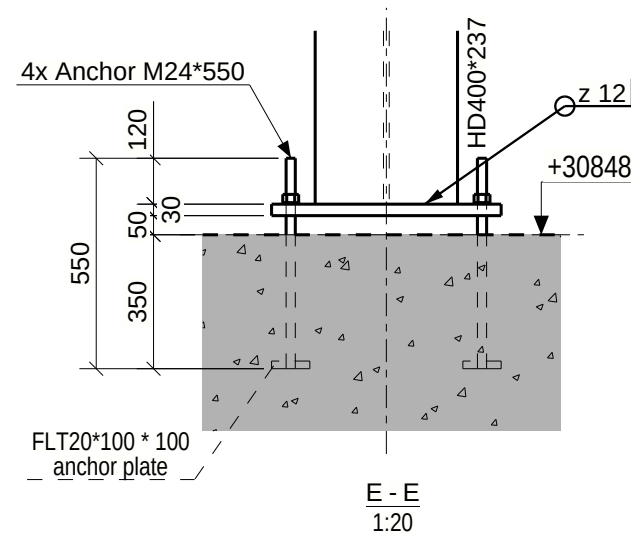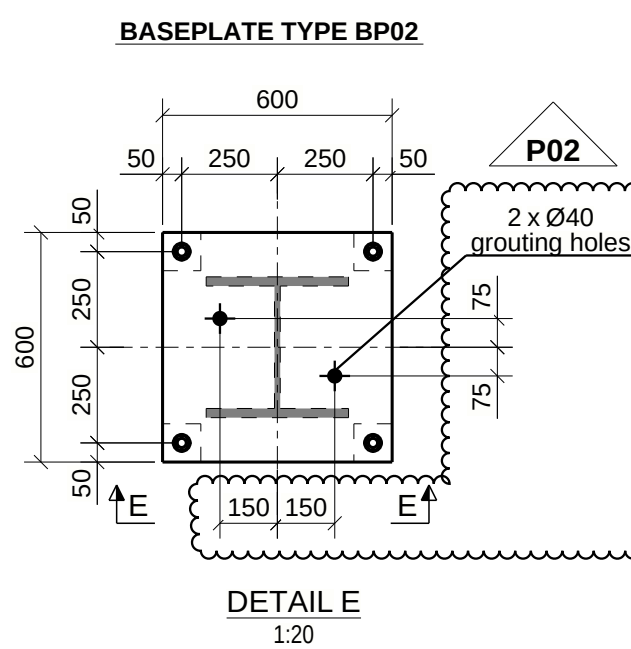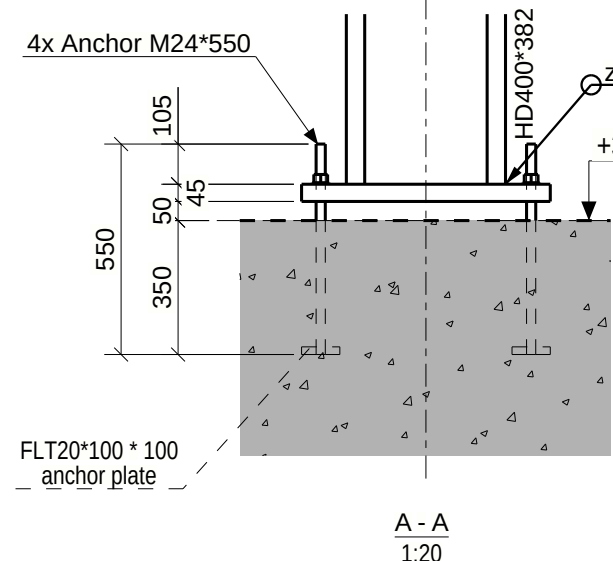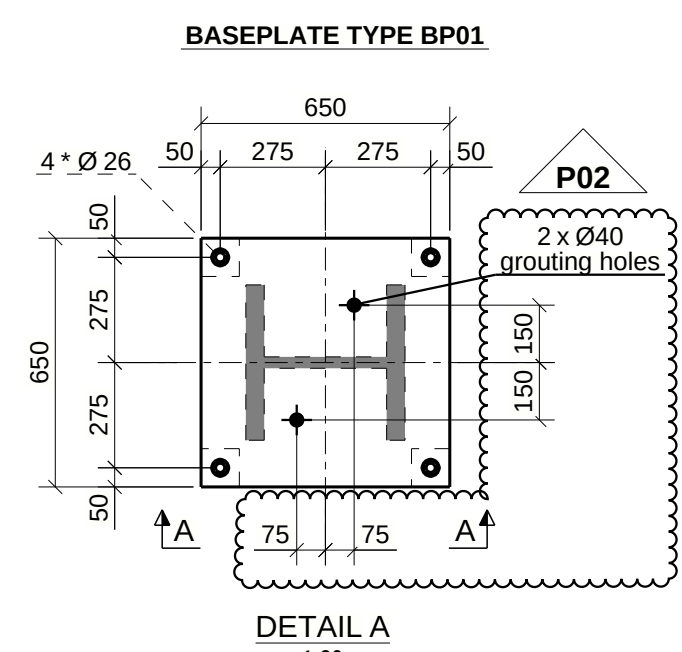

P02	REVISED AS NOTED	SF	09/12/25	EC	09/12/25
P01	FOR APPROVAL	SF	12/11/25	EC	12/11/25
Rev.	Description	Drawn By	Chkd by	Date	Date

**Severfield**

Severfield Commercial & Industrial Ltd
Severfield Nuclear & Infrastructure Ltd
Severfield Products & Processing Ltd
www.severfield.com

Client: TSL
Architect:
Engineer:

Project: STB1A


Drawing title: BASEPLATES MAIN COLUMNS DHC-1
GRIDLINE C-E
151

Dwn By: SF Chkd by: EC Appvd by: Scale: 1:20 1:90 1:200
Date: 03/11/25 Date: 12/11/25 Date:

SEVERFIELD PROJECT NO: C2147

Status Code:

Drawing No: STB1A-2.1-S-1011-DCH Rev: P02

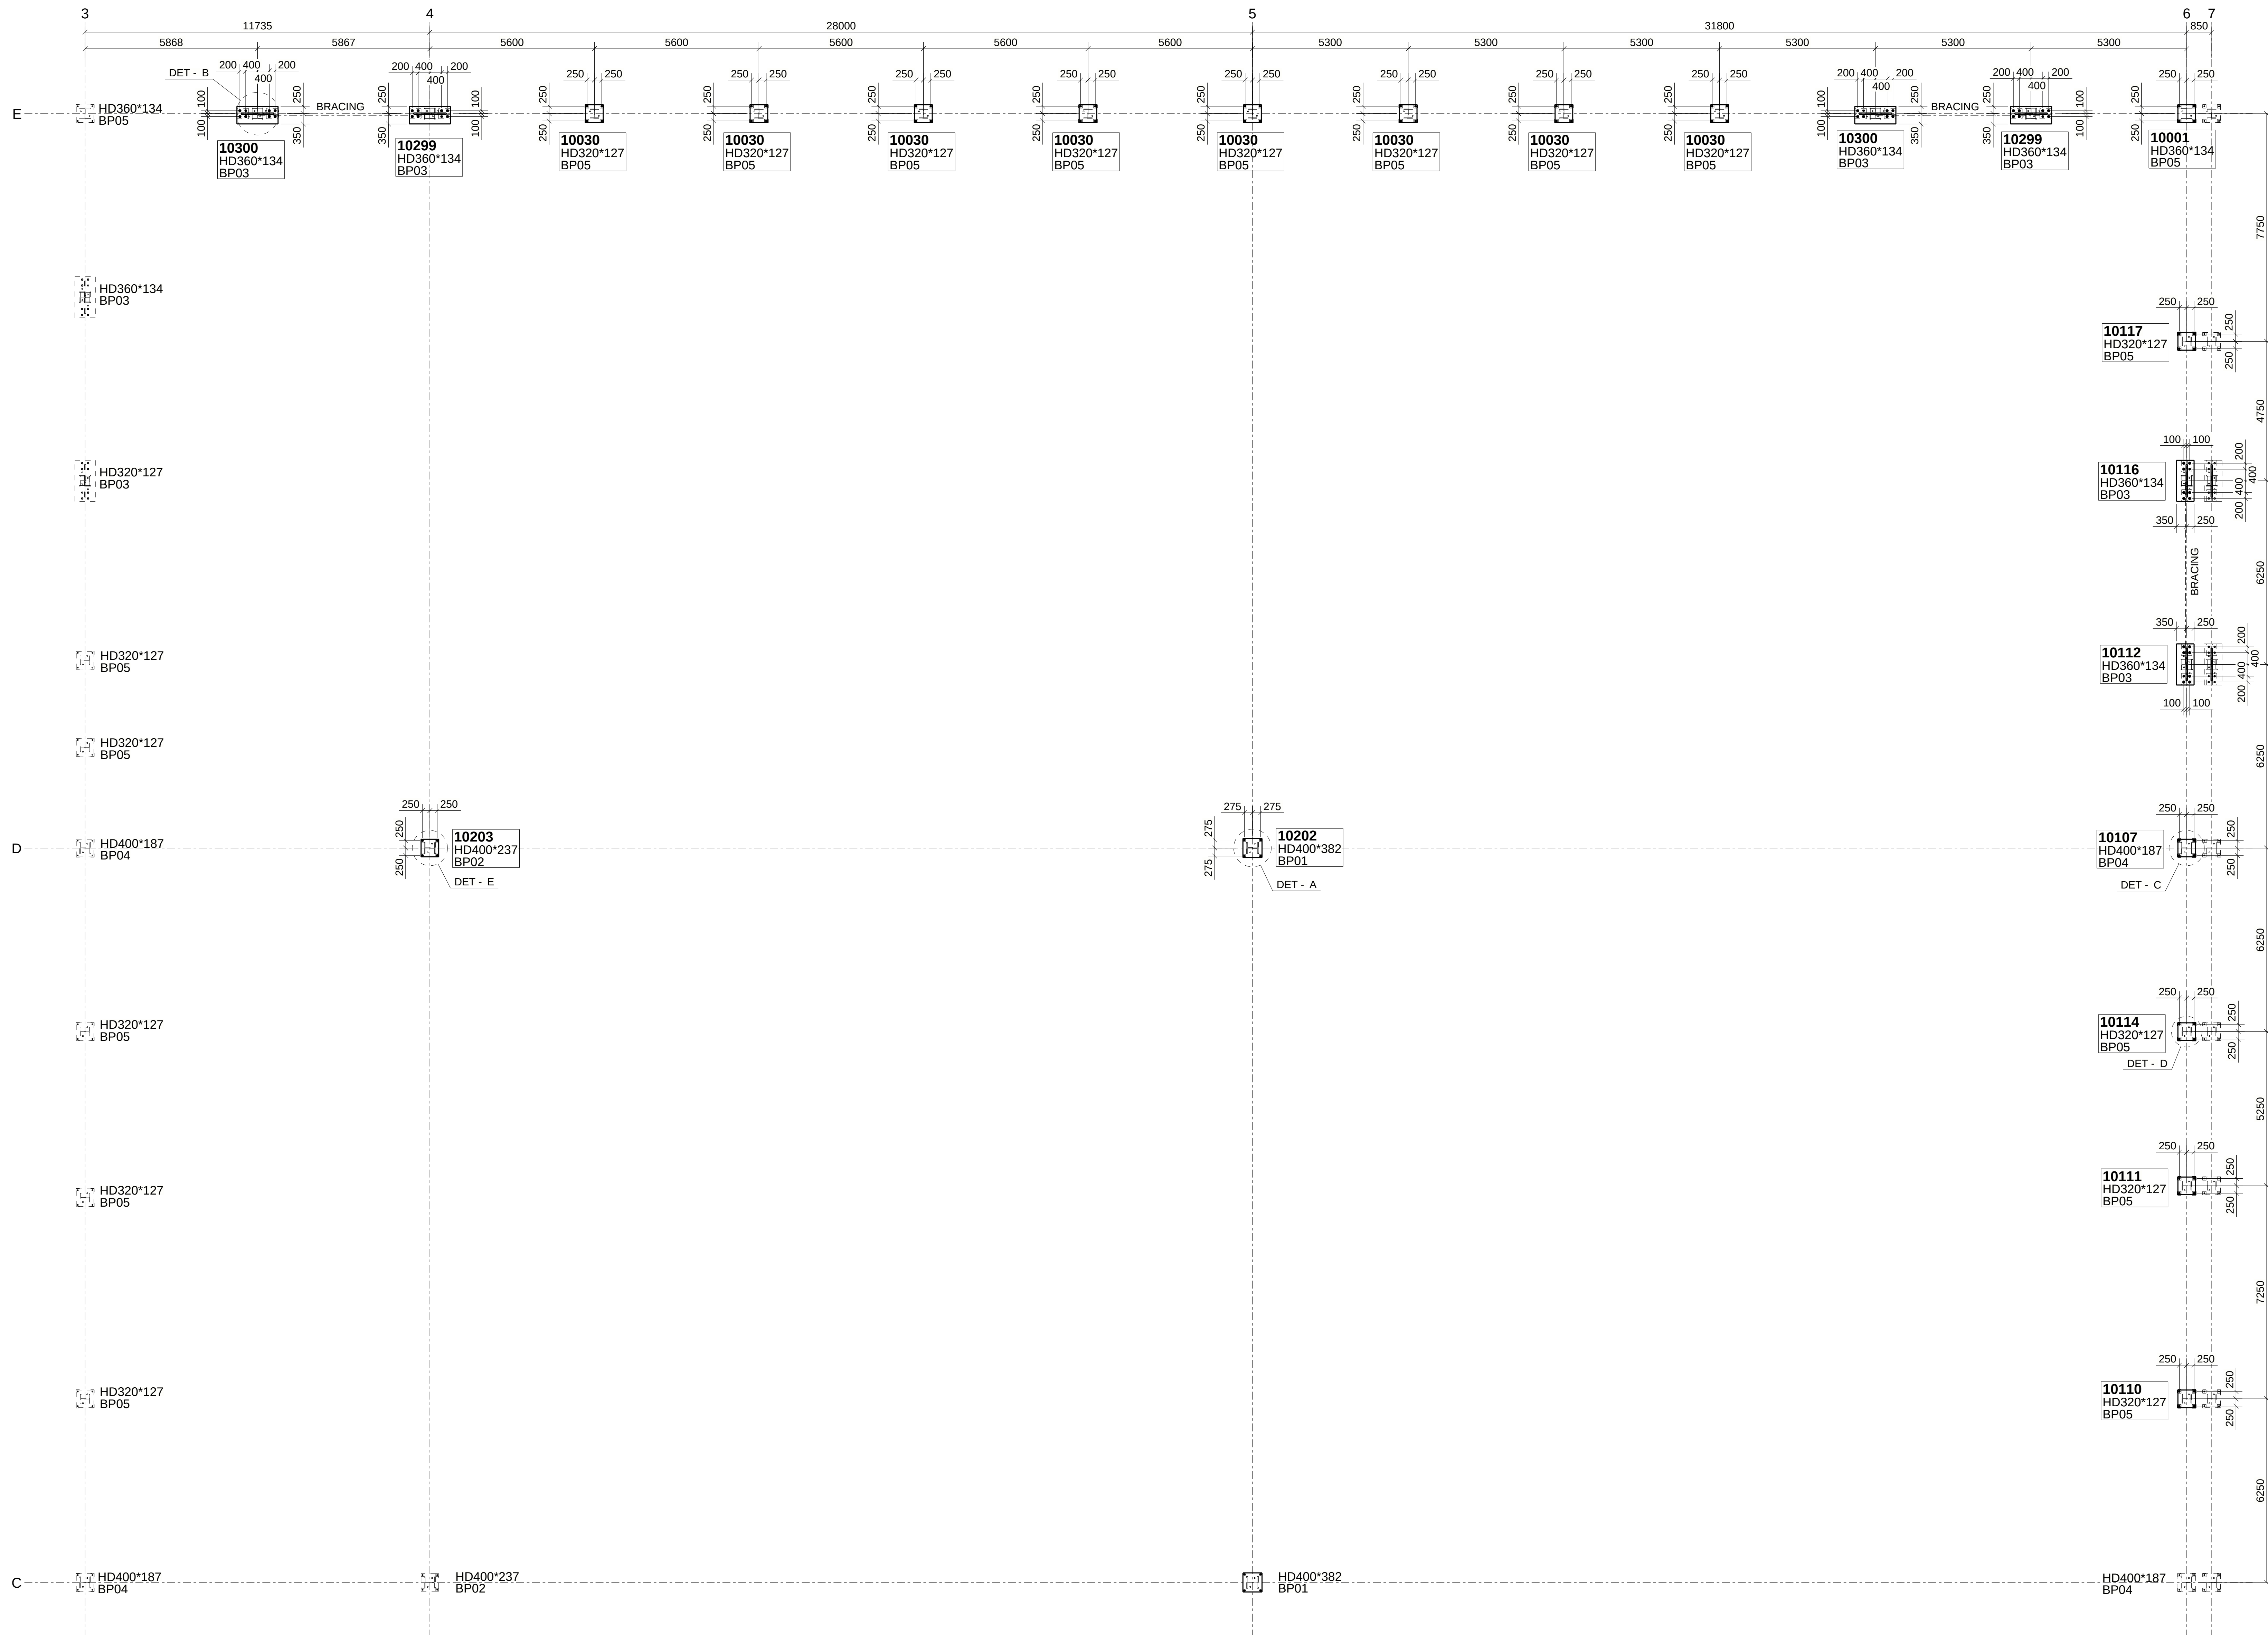

TOP VIEW BASEPLATES
1:90