


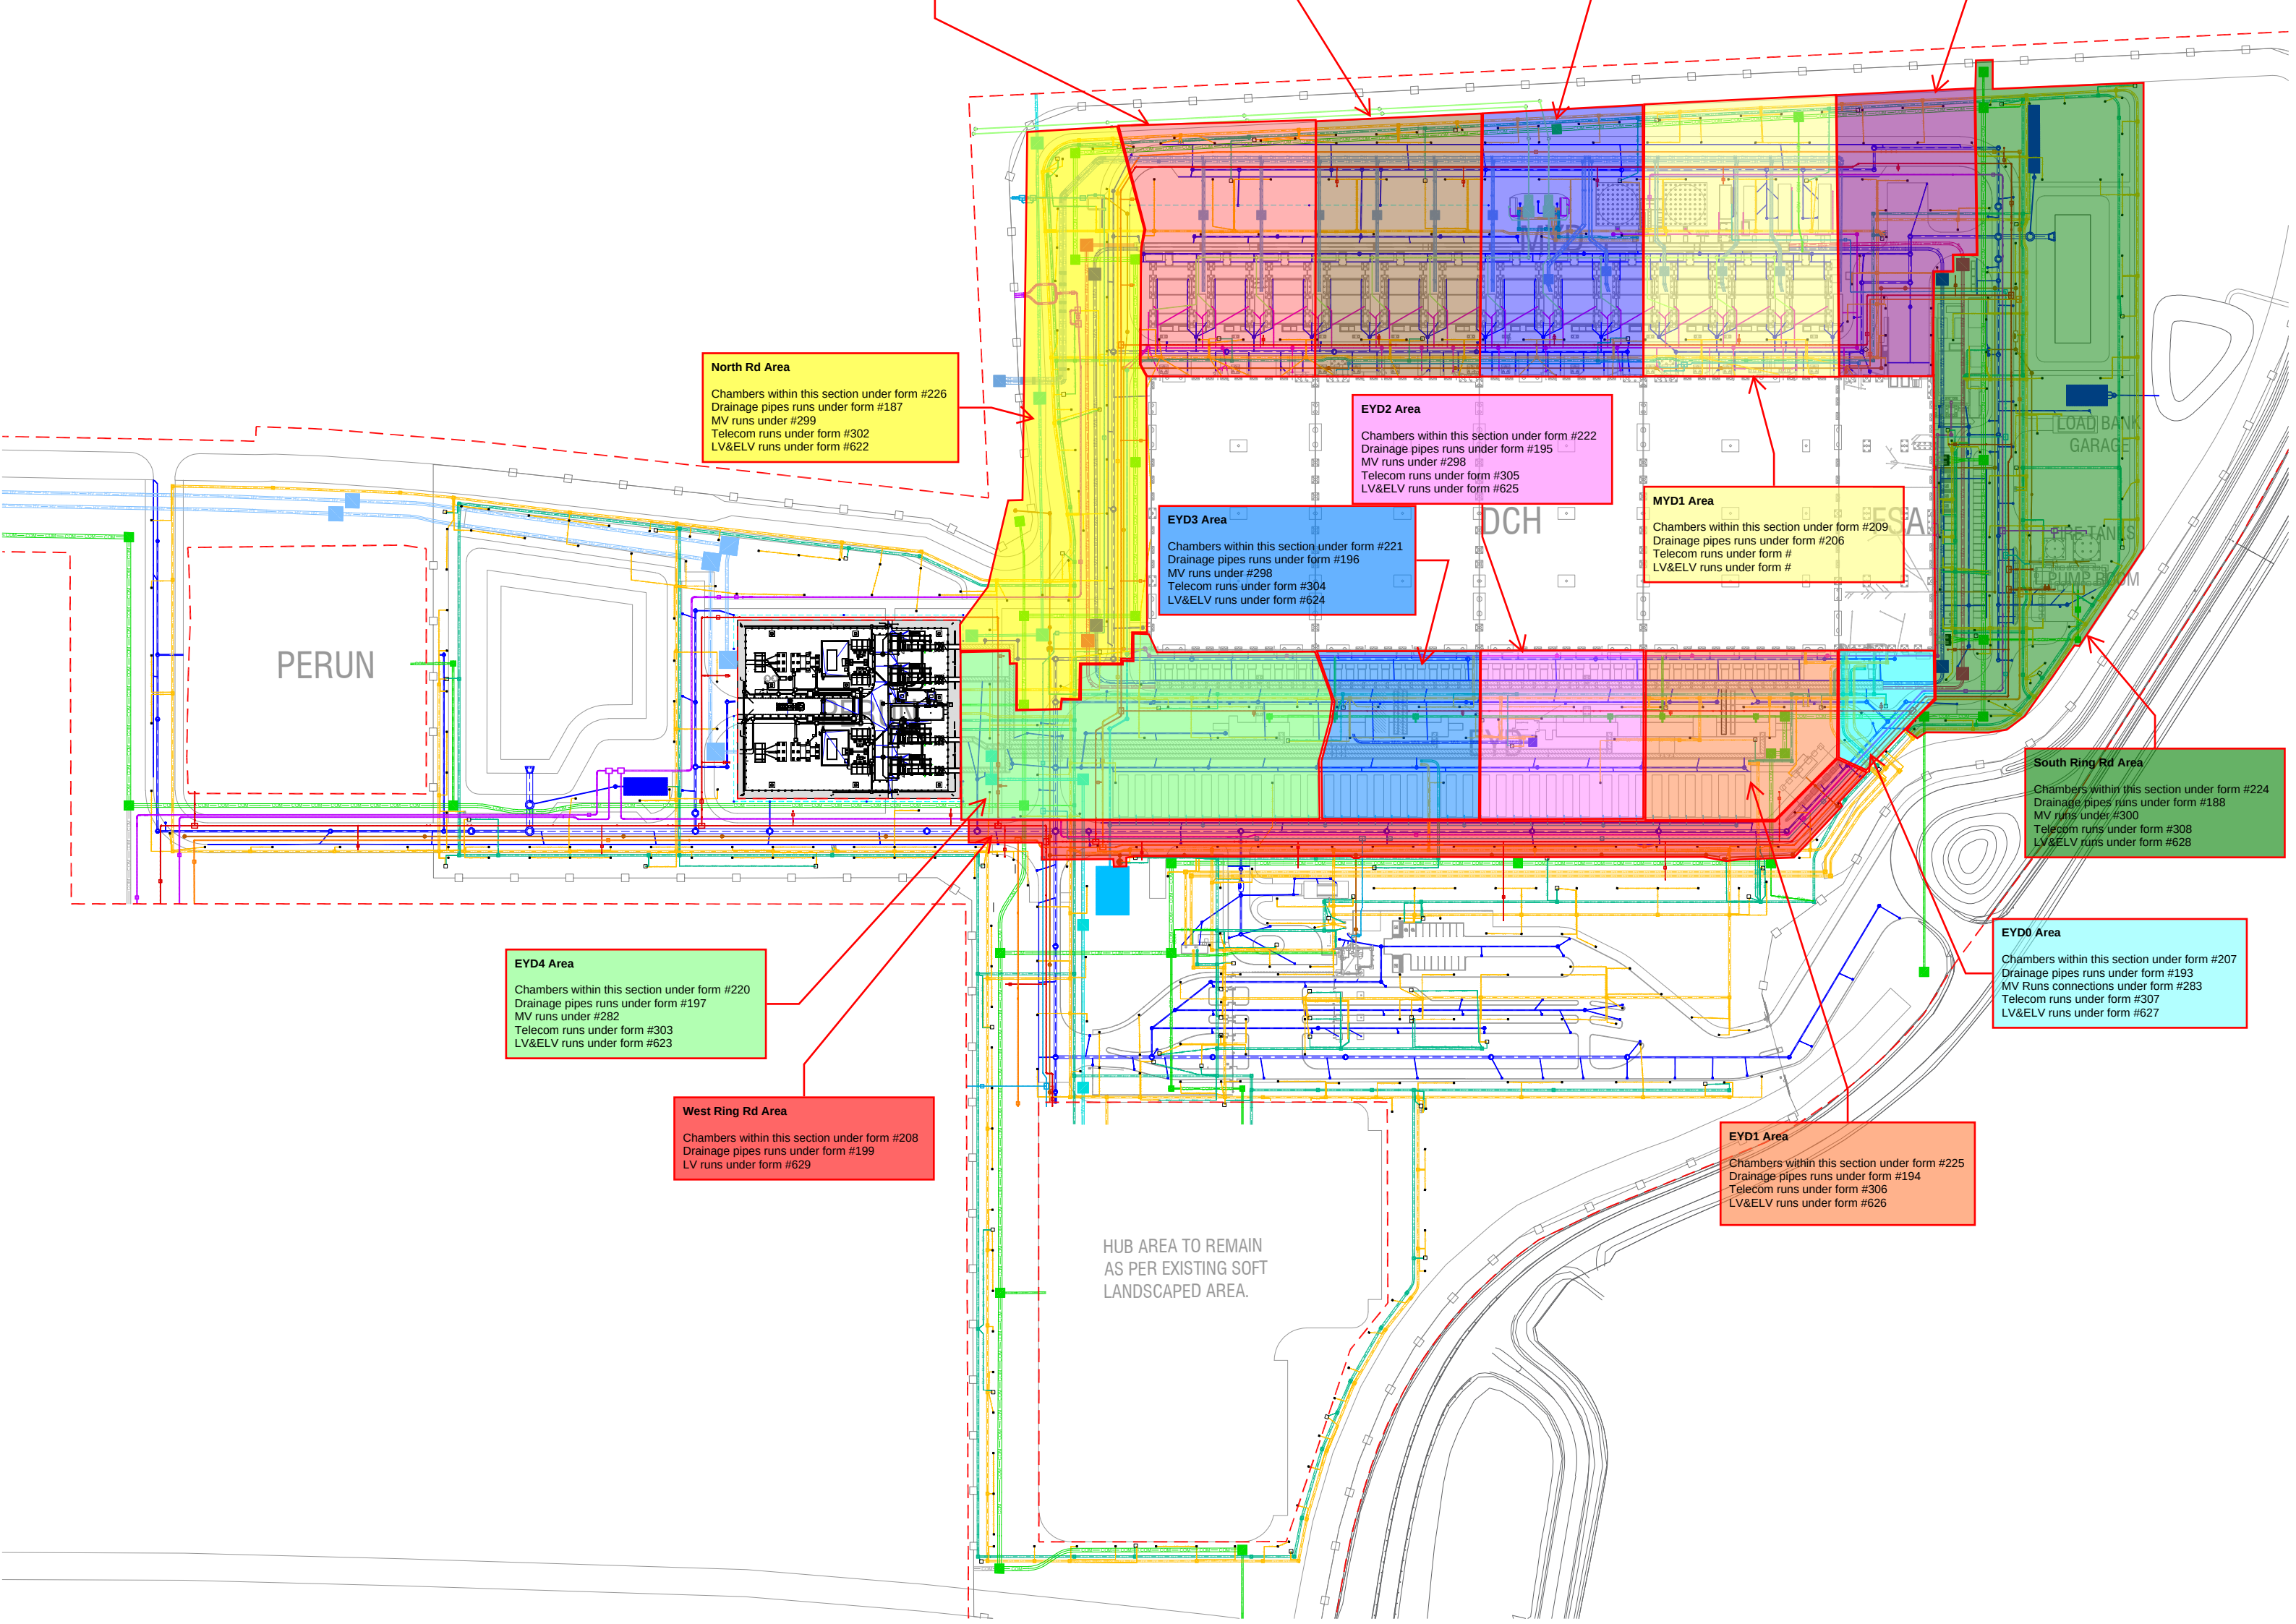

North Rd Area

Chambers within this section under form #226
Drainage pipes runs under form #187
MV runs under #299
Telecom runs under form #302
LV&ELV runs under form #622

EYD2 Area

Chambers within this section under form #222
Drainage pipes runs under form #195
MV runs under #298
Telecom runs under form #305
LV&ELV runs under form #625

EYD3 Area

Chambers within this section under form #221
Drainage pipes runs under form #196
MV runs under #298
Telecom runs under form #304
LV&ELV runs under form #624

MYD1 Area

Chambers within this section under form #209
Drainage pipes runs under form #206
Telecom runs under form #
LV&ELV runs under form #

South Ring Rd Area

Chambers within this section under form #224
Drainage pipes runs under form #188
MV runs under #300
Telecom runs under form #308
LV&ELV runs under form #628

EYD0 Area

Chambers within this section under form #207
Drainage pipes runs under form #193
MV Runs connections under form #283
Telecom runs under form #307
LV&ELV runs under form #627

EYD1 Area

Chambers within this section under form #225
Drainage pipes runs under form #194
Telecom runs under form #306
LV&ELV runs under form #626

West Ring Rd Area

Chambers within this section under form #208
Drainage pipes runs under form #199
LV runs under form #629

EYD4 Area

Chambers within this section under form #220
Drainage pipes runs under form #197
MV runs under #282
Telecom runs under form #303
LV&ELV runs under form #623

HUB AREA TO REMAIN
AS PER EXISTING SOFT
LANDSCAPED AREA.