

Chambers included within this area:

LV73, LV31, LV74, LV198, LV195, LV162, LV237, LV236, LV96, LV60, LV59, LV61, LV77, LV75, LV56, LV57, LV58, LV84, LV240, LV76, LV36, LV53, LV54, LV159, LV64, LV89, LV90;

ELV94, ELV46, ELV45, ELV121, ELV111, ELV120, ELV118, ELV112, ELV52, ELV110, ELV42, ELV93, ELV53, ELV 41, ELV92, ELV66;

MV18, MV9;


CV0195, CV0190, CV0185, CV0180, CV0175, CV0170, CV0165, CV0205;

FW17, FW31, FWIC6;

SW24, SW123, SW15, SW87, SW48, SW19, SW18, SW49, SW50, SW51, SW52, SW53, SW54, SW55, SW96, SW20, SW25, SW21, SW95, SW176, SW177, SW101, SW152, SW26, SW151, SW150, SW23, SW27, SW149, SW104, SW155, SW28, SW17, SW103;

Contaminated: SW MH123, SW MH122, SW MH120, SW MH127, SW MH128, SW MH129, SW MH130, SW MH119;

IW5, IW6, IW18, IW7, IW8;

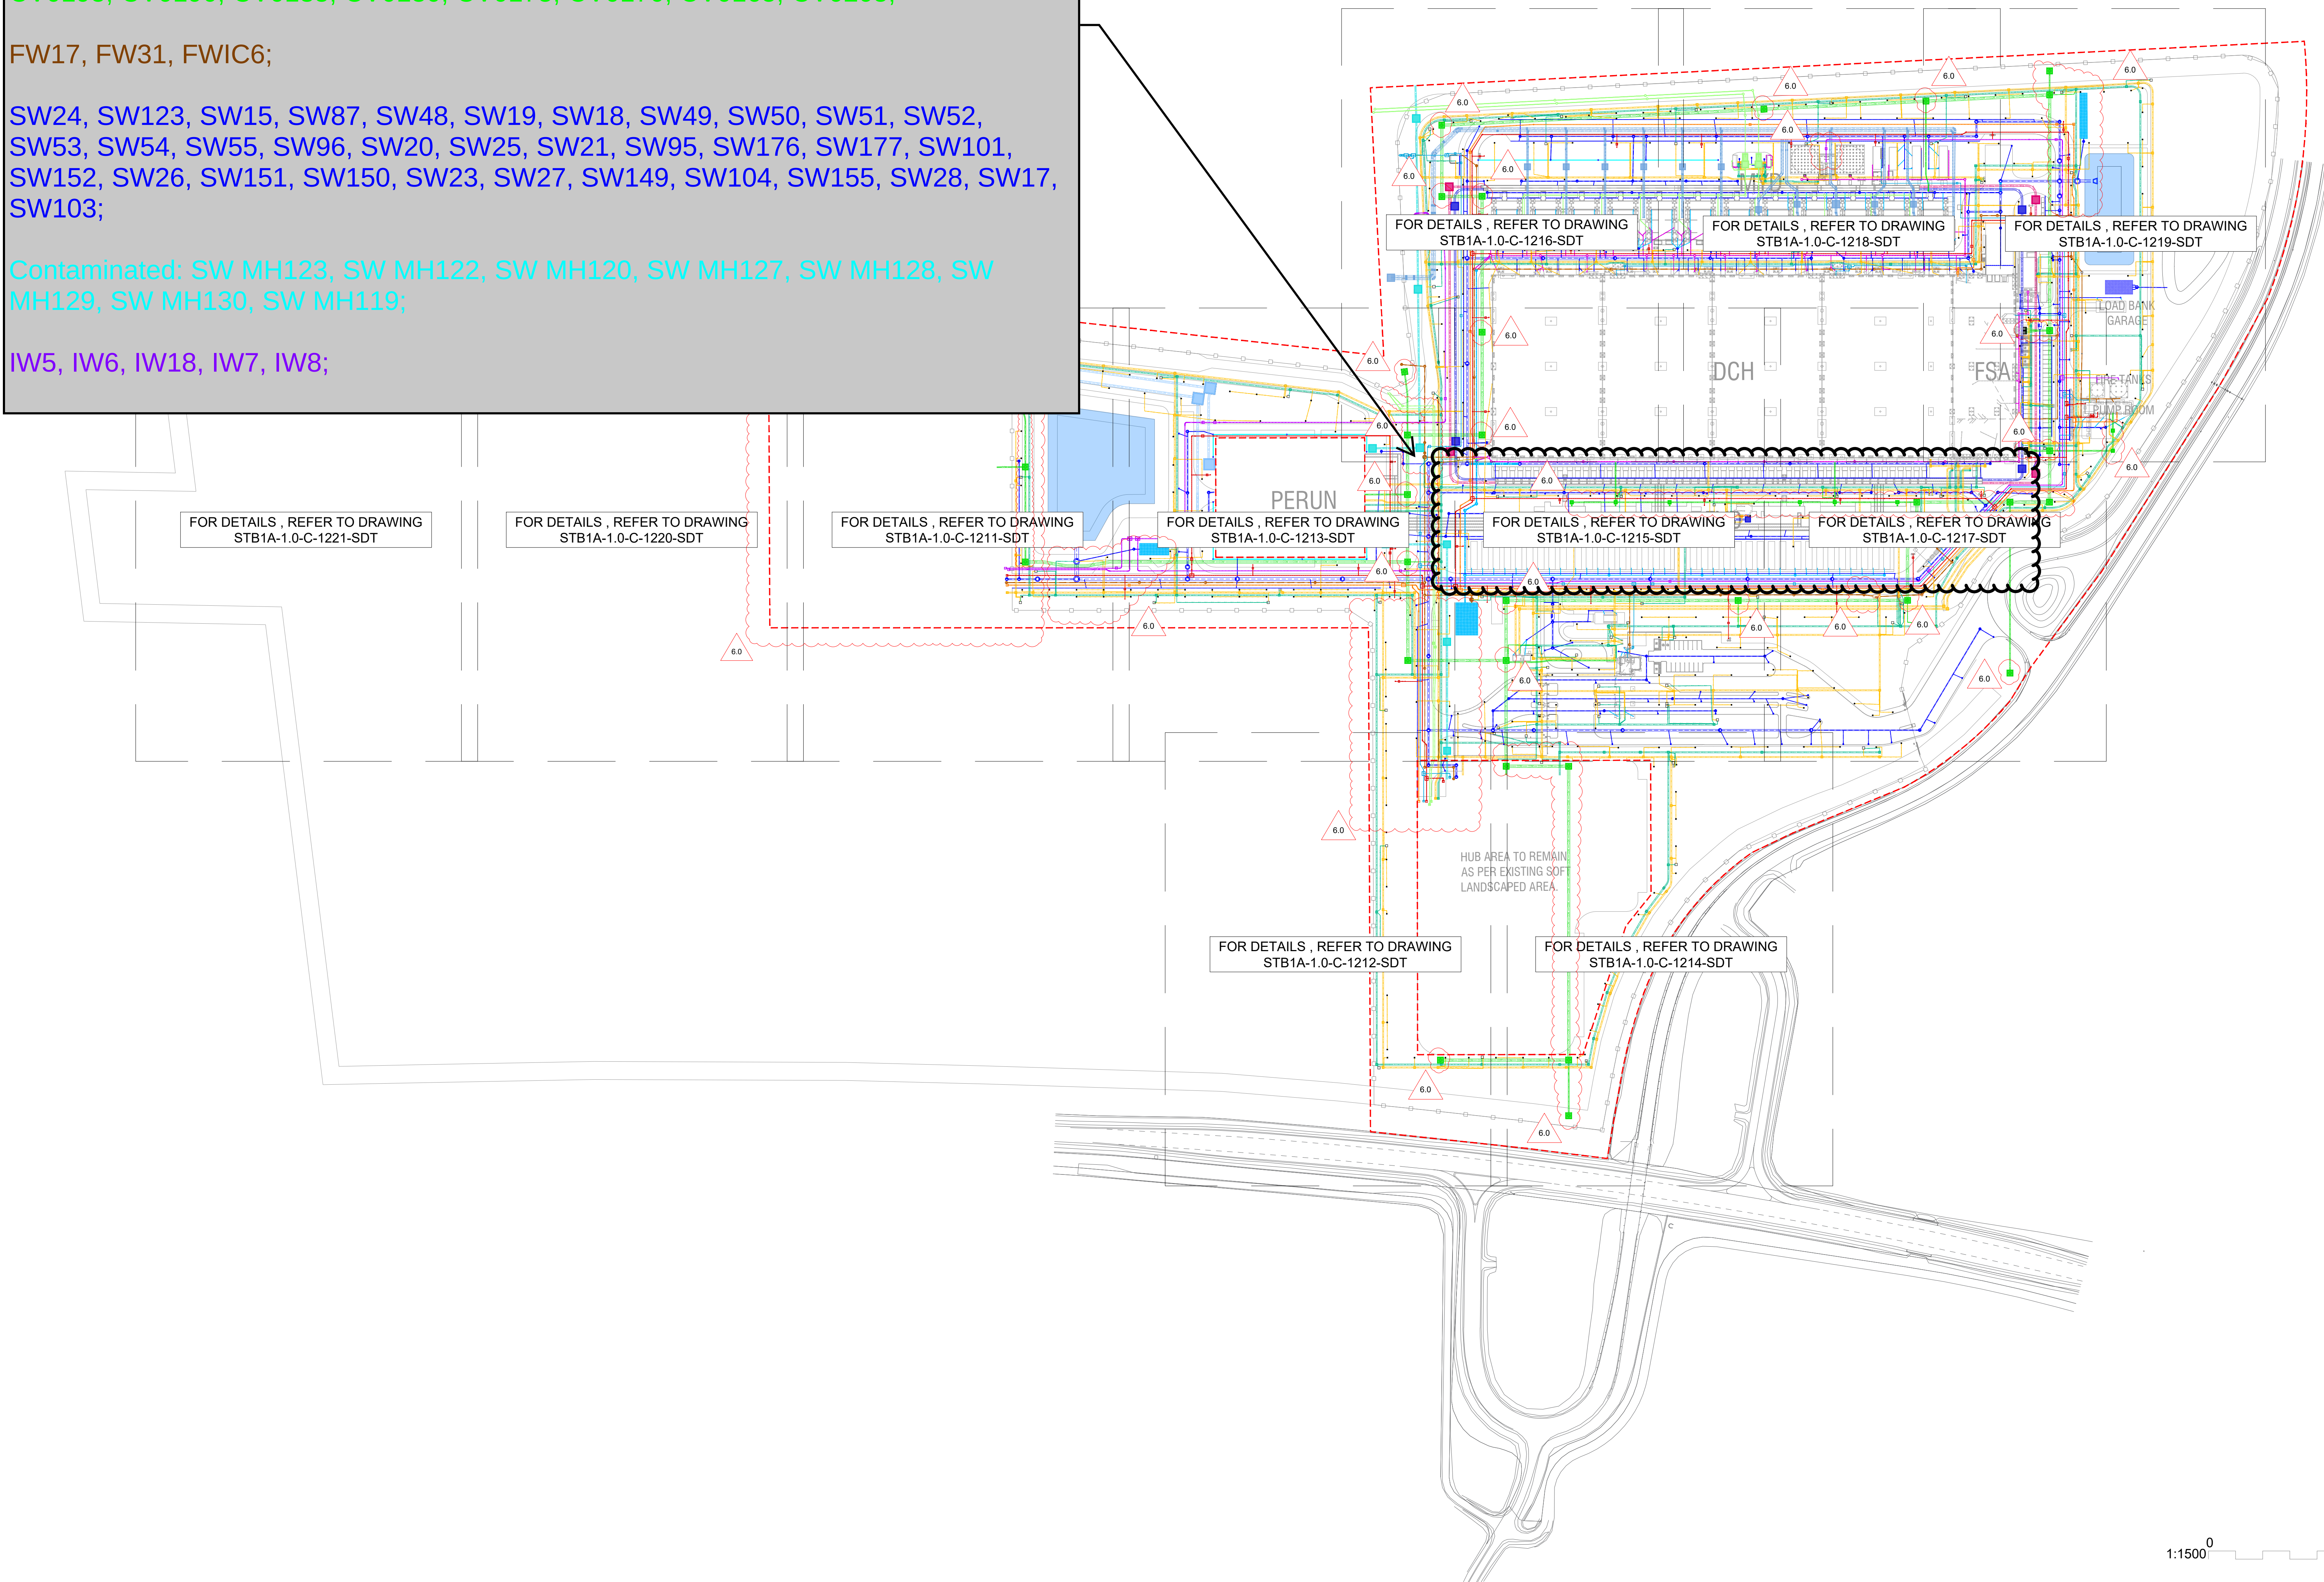

NOTES:

- DO NOT SCALE FROM THIS DRAWING. ALL DIMENSIONS INDICATED ARE IN METRES UNLESS OTHERWISE STATED. VALIDATE ALL MEASUREMENTS ON SITE.
- ANY DISCREPANCIES BETWEEN THE DRAWINGS AND OTHER DOCUMENTS SHOULD BE BROUGHT TO THE ATTENTION OF THE ENGINEER.
- THIS DRAWING IS NOT AN INSTALLATION DRAWING. IT IS THE CONTRACTORS RESPONSIBILITY TO MAKE FINAL COORDINATED INSTALLATION SHOP DRAWINGS.
- ALL ISSUED 3D MODEL FILES TAKE DESIGN PRIORITY OVER 2D DRAWINGS.
- THE CONTENTS OF THIS DRAWING SHALL BE READ IN CONJUNCTION WITH THE CURRENT REVISIONS OF ARCHITECTURAL, CIVIL, STRUCTURAL, MECHANICAL, ELECTRICAL, SECURITY, TELECOMS DRAWINGS AND ALL RELEVANT SECTIONS OF THE SPECIFICATIONS.

LEGEND

---	STB1A WORKING AREA BOUNDARY
- - - - -	STB1A PROPOSED FENCE LINE
---	SURFACE WATER DRAINAGE
---	SURFACE WATER CONTAMINATED
---	SURFACE WATER DRAINAGE CHANNEL / HERS DRAIN
---	SURFACE WATER PERFORATED PIPE
---	FOUL WATER DRAINAGE
---	FOUL WATER RISING MAIN
---	FOUL WATER DRAINAGE CHANNEL
---	INDUSTRIAL DRAINAGE
---	TELECOMMUNICATION
---	EXTRA LOW VOLTAGE NETWORK
---	LOW VOLTAGE NETWORK
---	MEDIUM VOLTAGE ROUTE A
---	MEDIUM VOLTAGE ROUTE B
---	MEDIUM VOLTAGE HUB
---	HIGH VOLTAGE 110kV
---	HEAT RECOVERY MAIN
---	BLOWDOWN WASTE
---	BLOWDOWN WASTE RISING MAIN
---	POTABLE WATER SUPPLY
---	RAW WATER INFLOW (COOLING)
---	HYDRANT MAIN
---	SPRINKLER MAIN
---	FOUL WATER DRAINAGE PUMPING STATION
---	SURFACE WATER CHAMBER
---	SURFACE WATER INSPECTION CHAMBER
---	SURFACE WATER CONTAMINATED CHAMBER
---	FOUL WATER CHAMBER
---	RAW WATER INFLOW (COOLING) CHAMBER
---	BLOWDOWN WASTE CHAMBER
---	HIGH VOLTAGE CHAMBER
---	MEDIUM VOLTAGE ROUTE A CHAMBER
---	MEDIUM VOLTAGE ROUTE B CHAMBER
---	SECURITY MEDIUM VOLTAGE CHAMBER
---	TELECOMMUNICATION CHAMBER
---	EXTRA LOW VOLTAGE CHAMBER
---	LOW VOLTAGE CHAMBER
---	FUEL INTERCEPTOR
---	FUEL RETENTION SEPARATOR
---	FIRE RETENTION TANK
---	GULLY
---	LIGHTING COLUMN
---	SAFETY BOLLARD
---	CCTV FOUNDATION
---	SOAKAWAY

ARCHITECTURE:

ARC:MC
140-142 St. John Street,
London, EC1V 4UB
United Kingdom
t: +44 (0) 203 411 2571
e: info@arcmc.co.uk



INFRASTRUCTURE / CIVILS:

SWECO
Eldon House
2-3 Eldon Street
London,
EC2M 7LS
+44 (0) 20 3002 1210
e: www.sweco.co.uk

MEP:

Black & White Engineering
69 Wilson Street,
London, EC2A 2BB
United Kingdom
t: +44 (0) 207 683 7166
e: londoneng@bw-engineering.com

STB1A - PUF - IFC FINAL ISSUE (ISSUE FOR CONTRACT) 2026-01-23

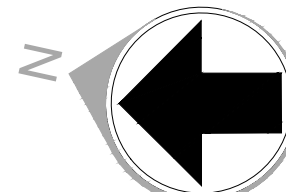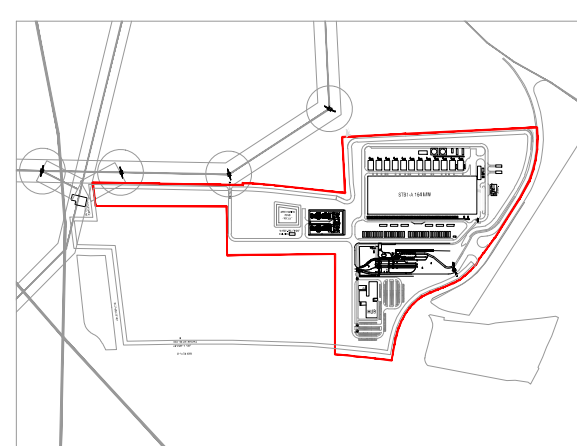

REVISIONS

NO.	DATE	DESCRIPTION
0.3	12/03/2025	DRAFT IFC UPDATES
1.0	11/04/2025	IFC FINAL ISSUE
1.1	30/05/2025	POST IFC DRAFT ISSUE
2.0	04/07/2025	POST IFC DRAFT ISSUE
2.1	05/08/2025	POST IFC DRAFT ISSUE
3.0	05/09/2025	POST IFC FINAL ISSUE
3.1	24/10/2025	POST IFC DRAFT ISSUE
4.0	07/11/2025	POST IFC FINAL ISSUE
5.0	08/01/2026	POST IFC DRAFT ISSUE
6.0	23/01/2026	POST IFC FINAL ISSUE

Drawn By:

MRP

Approved By:

AC

Design Team:

BW

STB1A

BUCKINGHAM

Project Number: 65212899

Proposed Combined Services Layout Overview

Discipline: Civil

Scale: 1:1500

Sheet Size: A0

Sheet Number:

STB1A-1.0-C-1210-SDT

Current Rev: 6.0

Phase: IFC

Drawing Name: STB1A-1.0-C-1210-SDT.dwg

Native File Format: Civil 3D V.2024